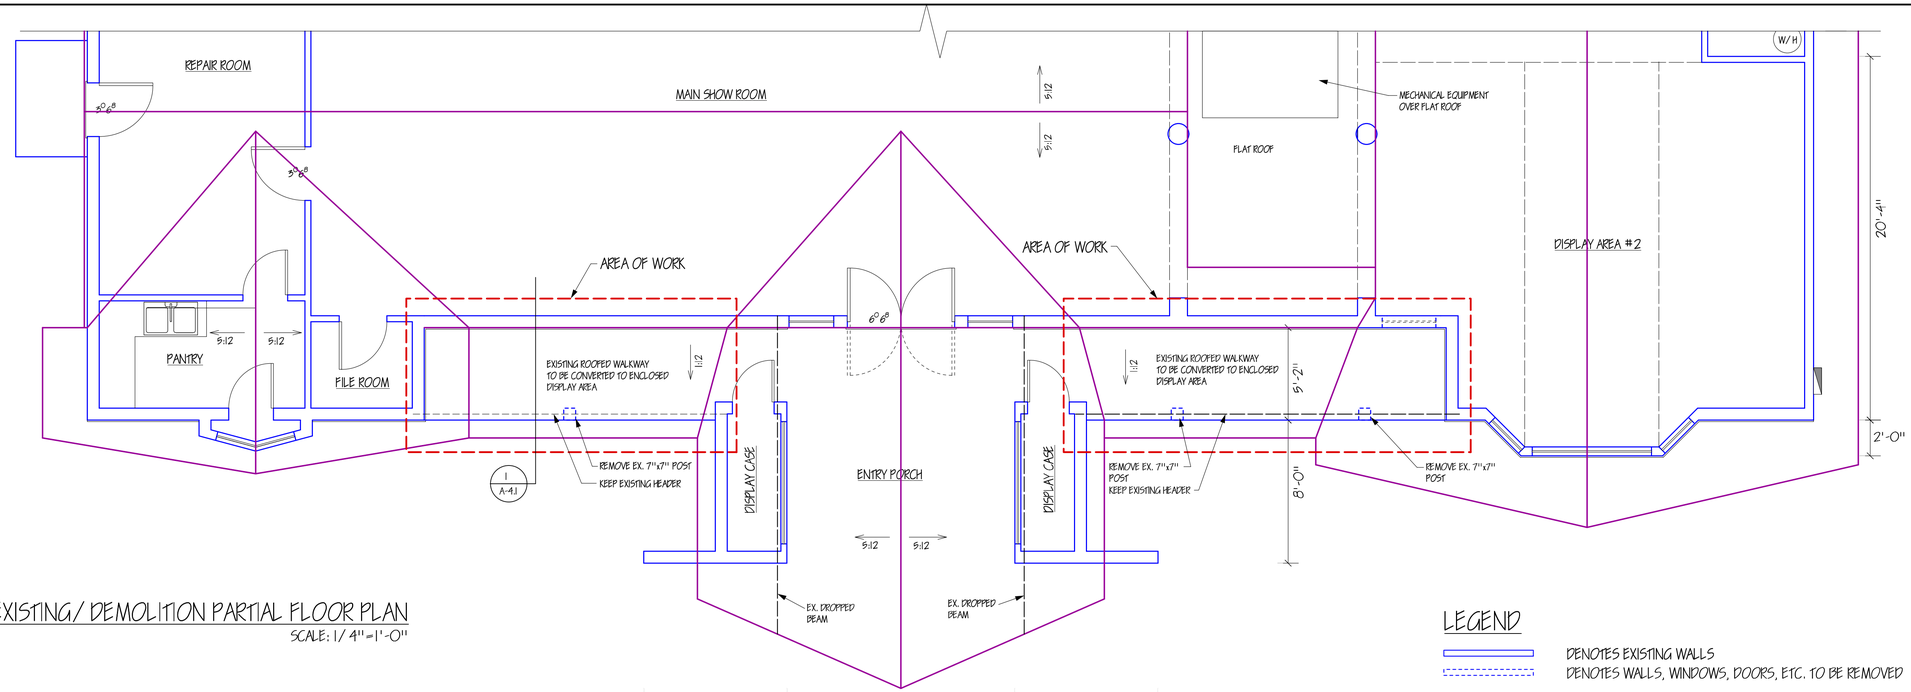



EXISTING/ DEMOLITION PARTIAL FLOOR PLAN

SCALE: 1/ 4"=1'-0"

LEGEND

DENOTES EXISTING WALLS

DENOTES WALLS, WINDOWS, DOORS, ETC. TO BE REMOVED

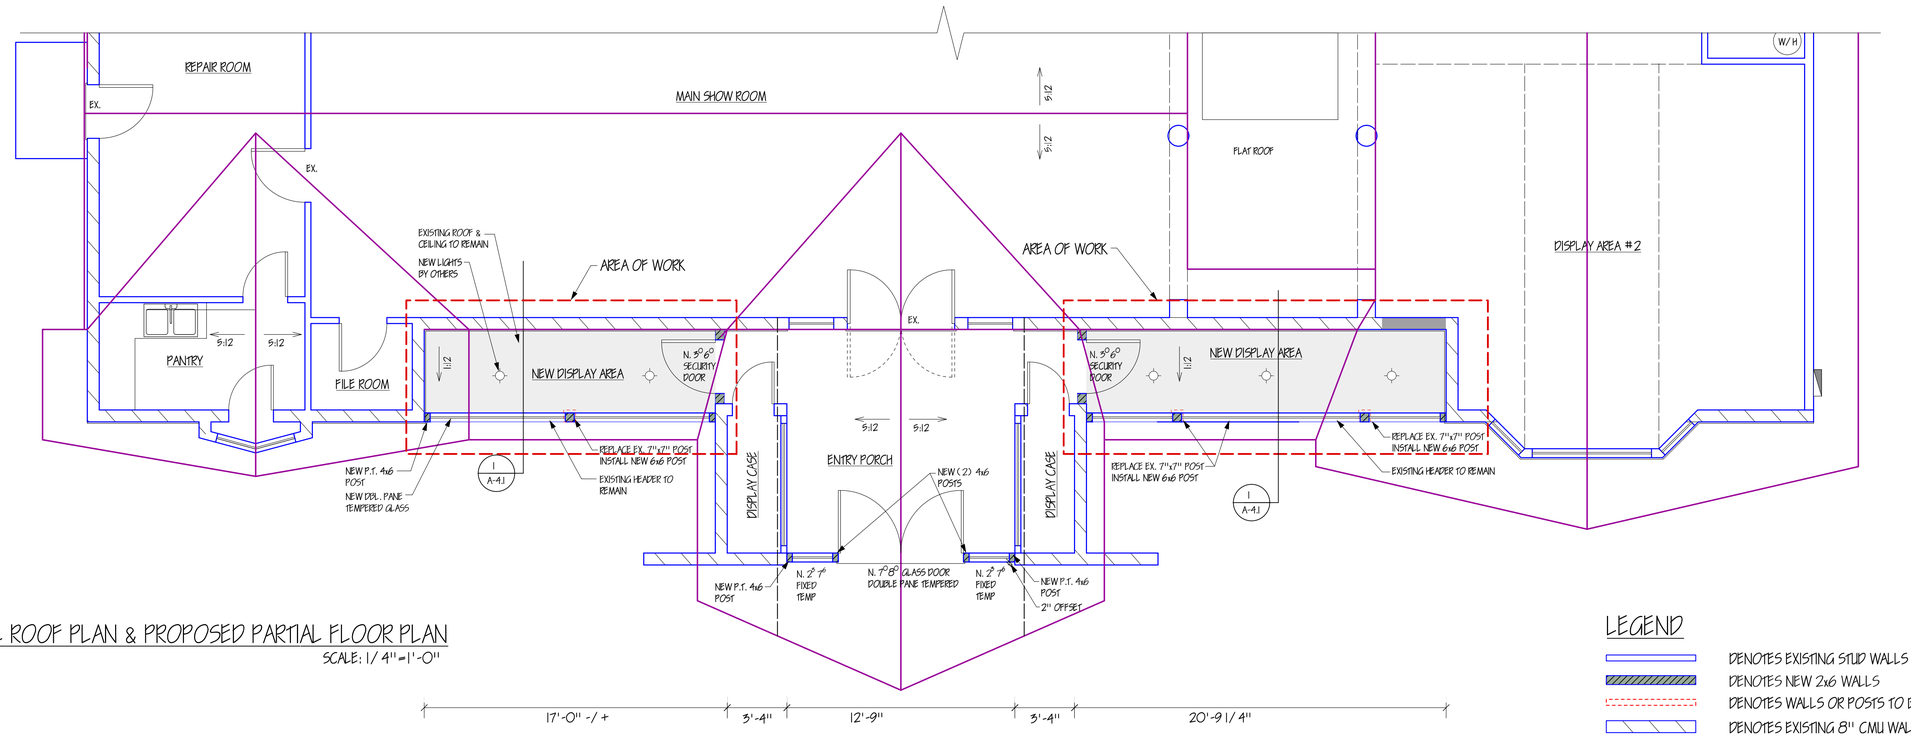

EXISTING PARTIAL ROOF PLAN & PROPOSED PARTIAL FLOOR PLAN

SCALE: 1/ 4"=1'-0"

LEGEND

DENOTES EXISTING STUD WALLS

DENOTES NEW 2x6 WALLS

DENOTES WALLS OR POSTS TO BE REMOVED

DENOTES EXISTING 8" CMU WALLS

PRELIMINARY NOT VALID FOR CONSTRUCTION
FOR BIDDING PURPOSES ONLY

ATA ENGINEERING
Ali Adib, P.E.
1202 Main Street, Redwood City, CA 94063
Tel. 650.363.2338, Fax 650.363.2031, email: ata@ataeng.net

EXISTING/DEMOLITION FLOOR PLAN

REGISTERED PROFESSIONAL ENGINEER
ALI ADIB
NO. CE49976
Exp. 6-30-25
CIVIL
STATE OF CALIFORNIA

REMODEL/ADDITION:
ADIB'S PERSIAN RUG CO
1426 S MAIN STREET
WALNUT CREEK,CA

DATE: 2024-08-05

A-1.1

OF SHEETS