



1 VICINITY MAP

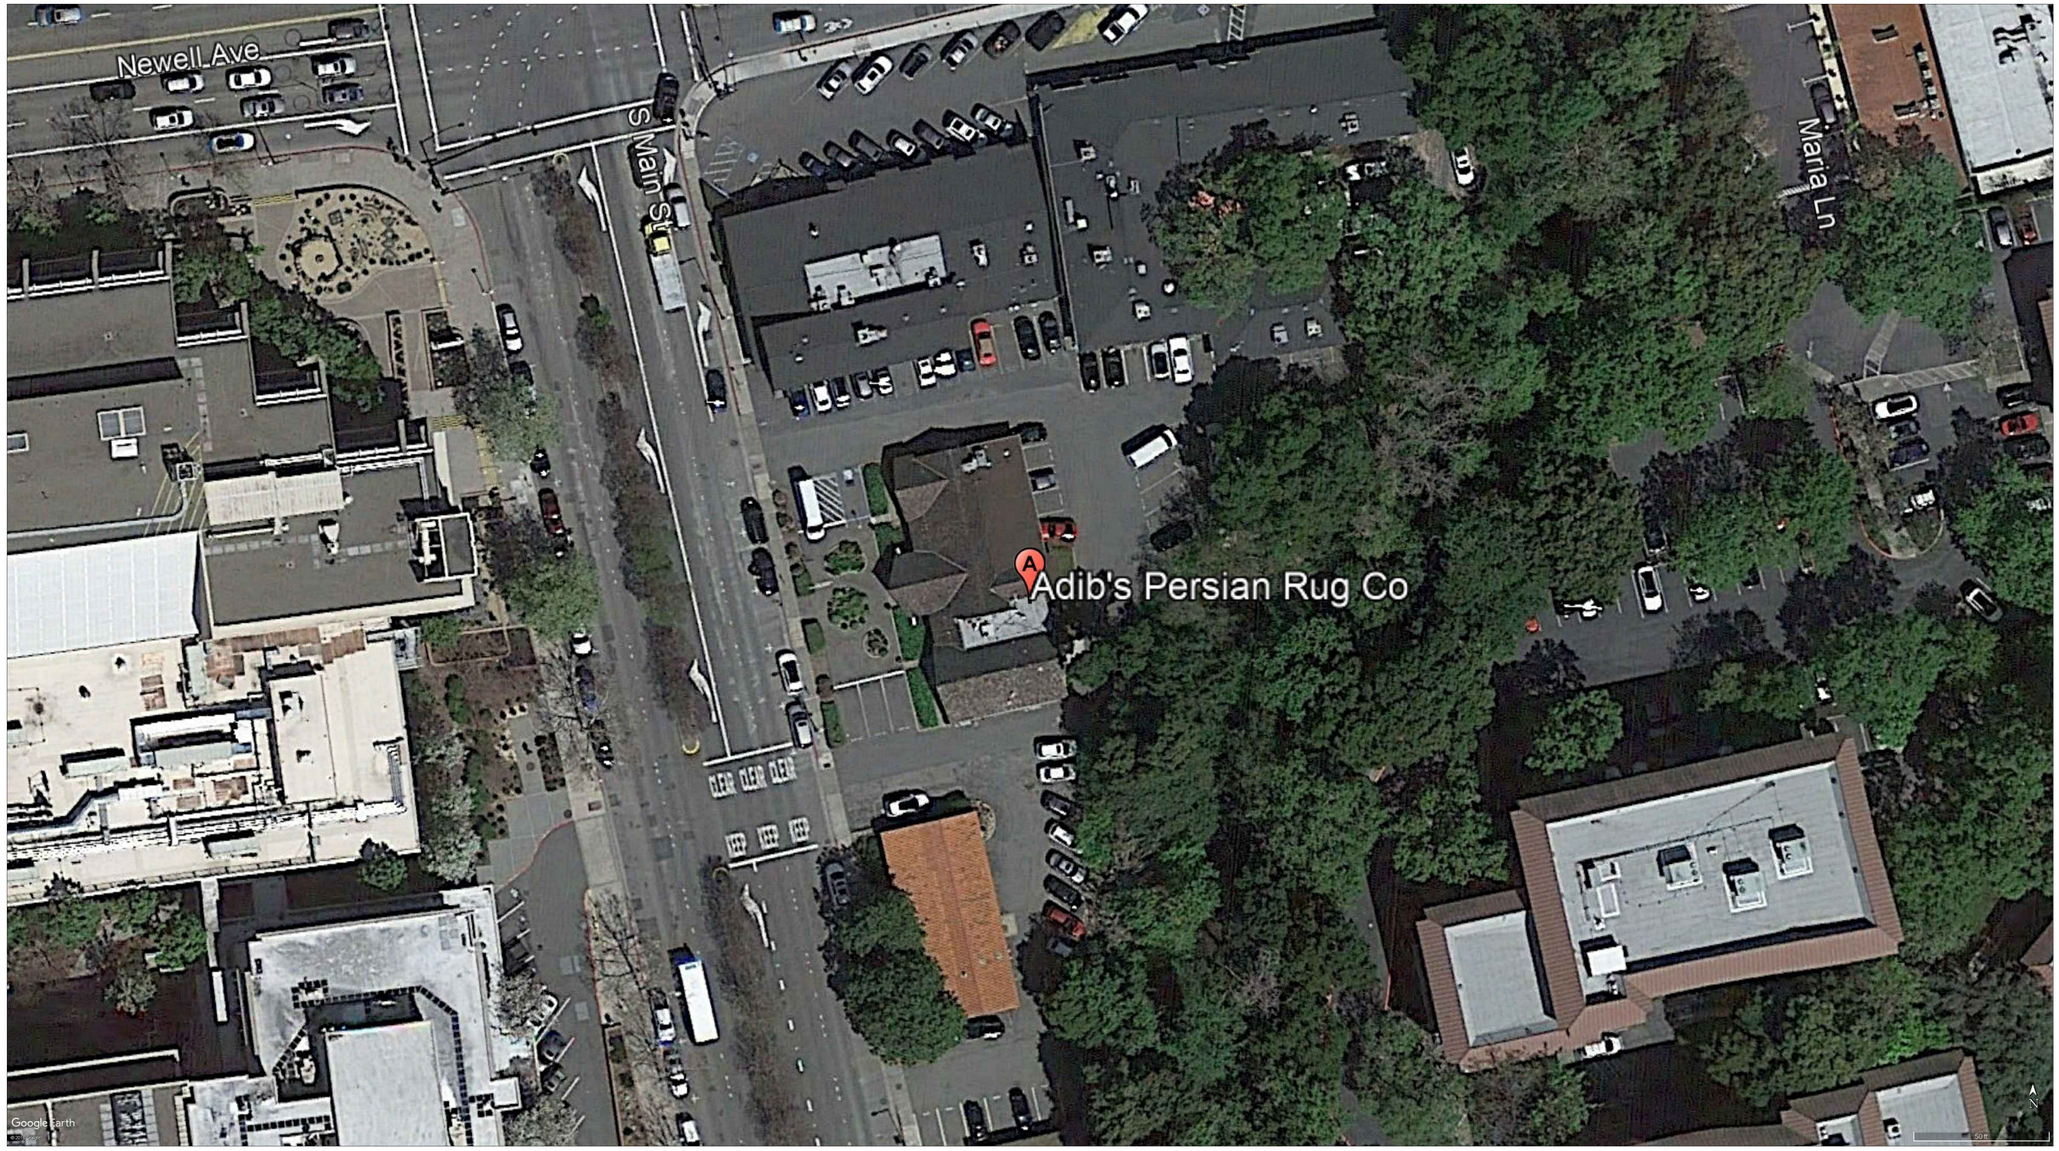


2 EXISTING STREET VIEW

# 1426 S. MAIN ST

## RETAIL & RESIDENTIAL ADDITION

### SHEET INDEX


G0 COVER SHEET, VICINITY MAP AND EXISTING STREET VIEW
G1 SURVEY
A1 OPTION A - SITE PLAN, 2ND LEVEL PLAN AND ELEVATION
A2 OPTION B - SITE PLAN, 2ND LEVEL PLAN AND ELEVATION
A3 OPTION C - SITE PLAN, 2ND LEVEL PLAN AND ELEVATION



LCA ARCHITECTS

WWW . LCA - ARCHITECTS . COM

CARL E. CAMPOS
DAVID BOOSTAD
PETER STACKPOLE

590 YGNACIO VALLEY ROAD, SUITE 310
WALNUT CREEK, CALIFORNIA 94596
(925) 944-1626

1970 BROADWAY, SUITE 800
OAKLAND, CALIFORNIA 94612
(510) 272-1060


1426 S. MAIN ST
RETAIL & RESIDENTIAL ADDITION


LCA ARCHITECTS
RESTRICTED ARCHITECTURAL DRAWINGS

THE INFORMATION, PLANS, DESIGNS, NOTES AND ARRANGEMENTS SHOWN ON THIS DRAWING ARE CONFIDENTIAL AND MAY NOT BE REPRODUCED IN WHOLE OR IN PART WITHOUT THE EXPRESSED WRITTEN PERMISSION OF LCA ARCHITECTS. DRAWINGS NOTED AS PRELIMINARY, SCHEMATIC AND / OR CONCEPT CONTAIN INFORMATION THAT IS CONCEPTUAL AND SUBJECT TO VERIFICATION AND/OR CHANGE. THE ARCHITECT MAKES NO CLAIM FOR ACCURACY OF CONCEPTUAL INFORMATION OR OF INFORMATION SUPPLIED BY OTHERS.



COVER SHEET
VICINITY MAP
EXISTING ELEVATION

SCALE:
DATE: 06 / 19 / 2019
REVISIONS:

PROJECT NO. 13034

G0

SHEET OF

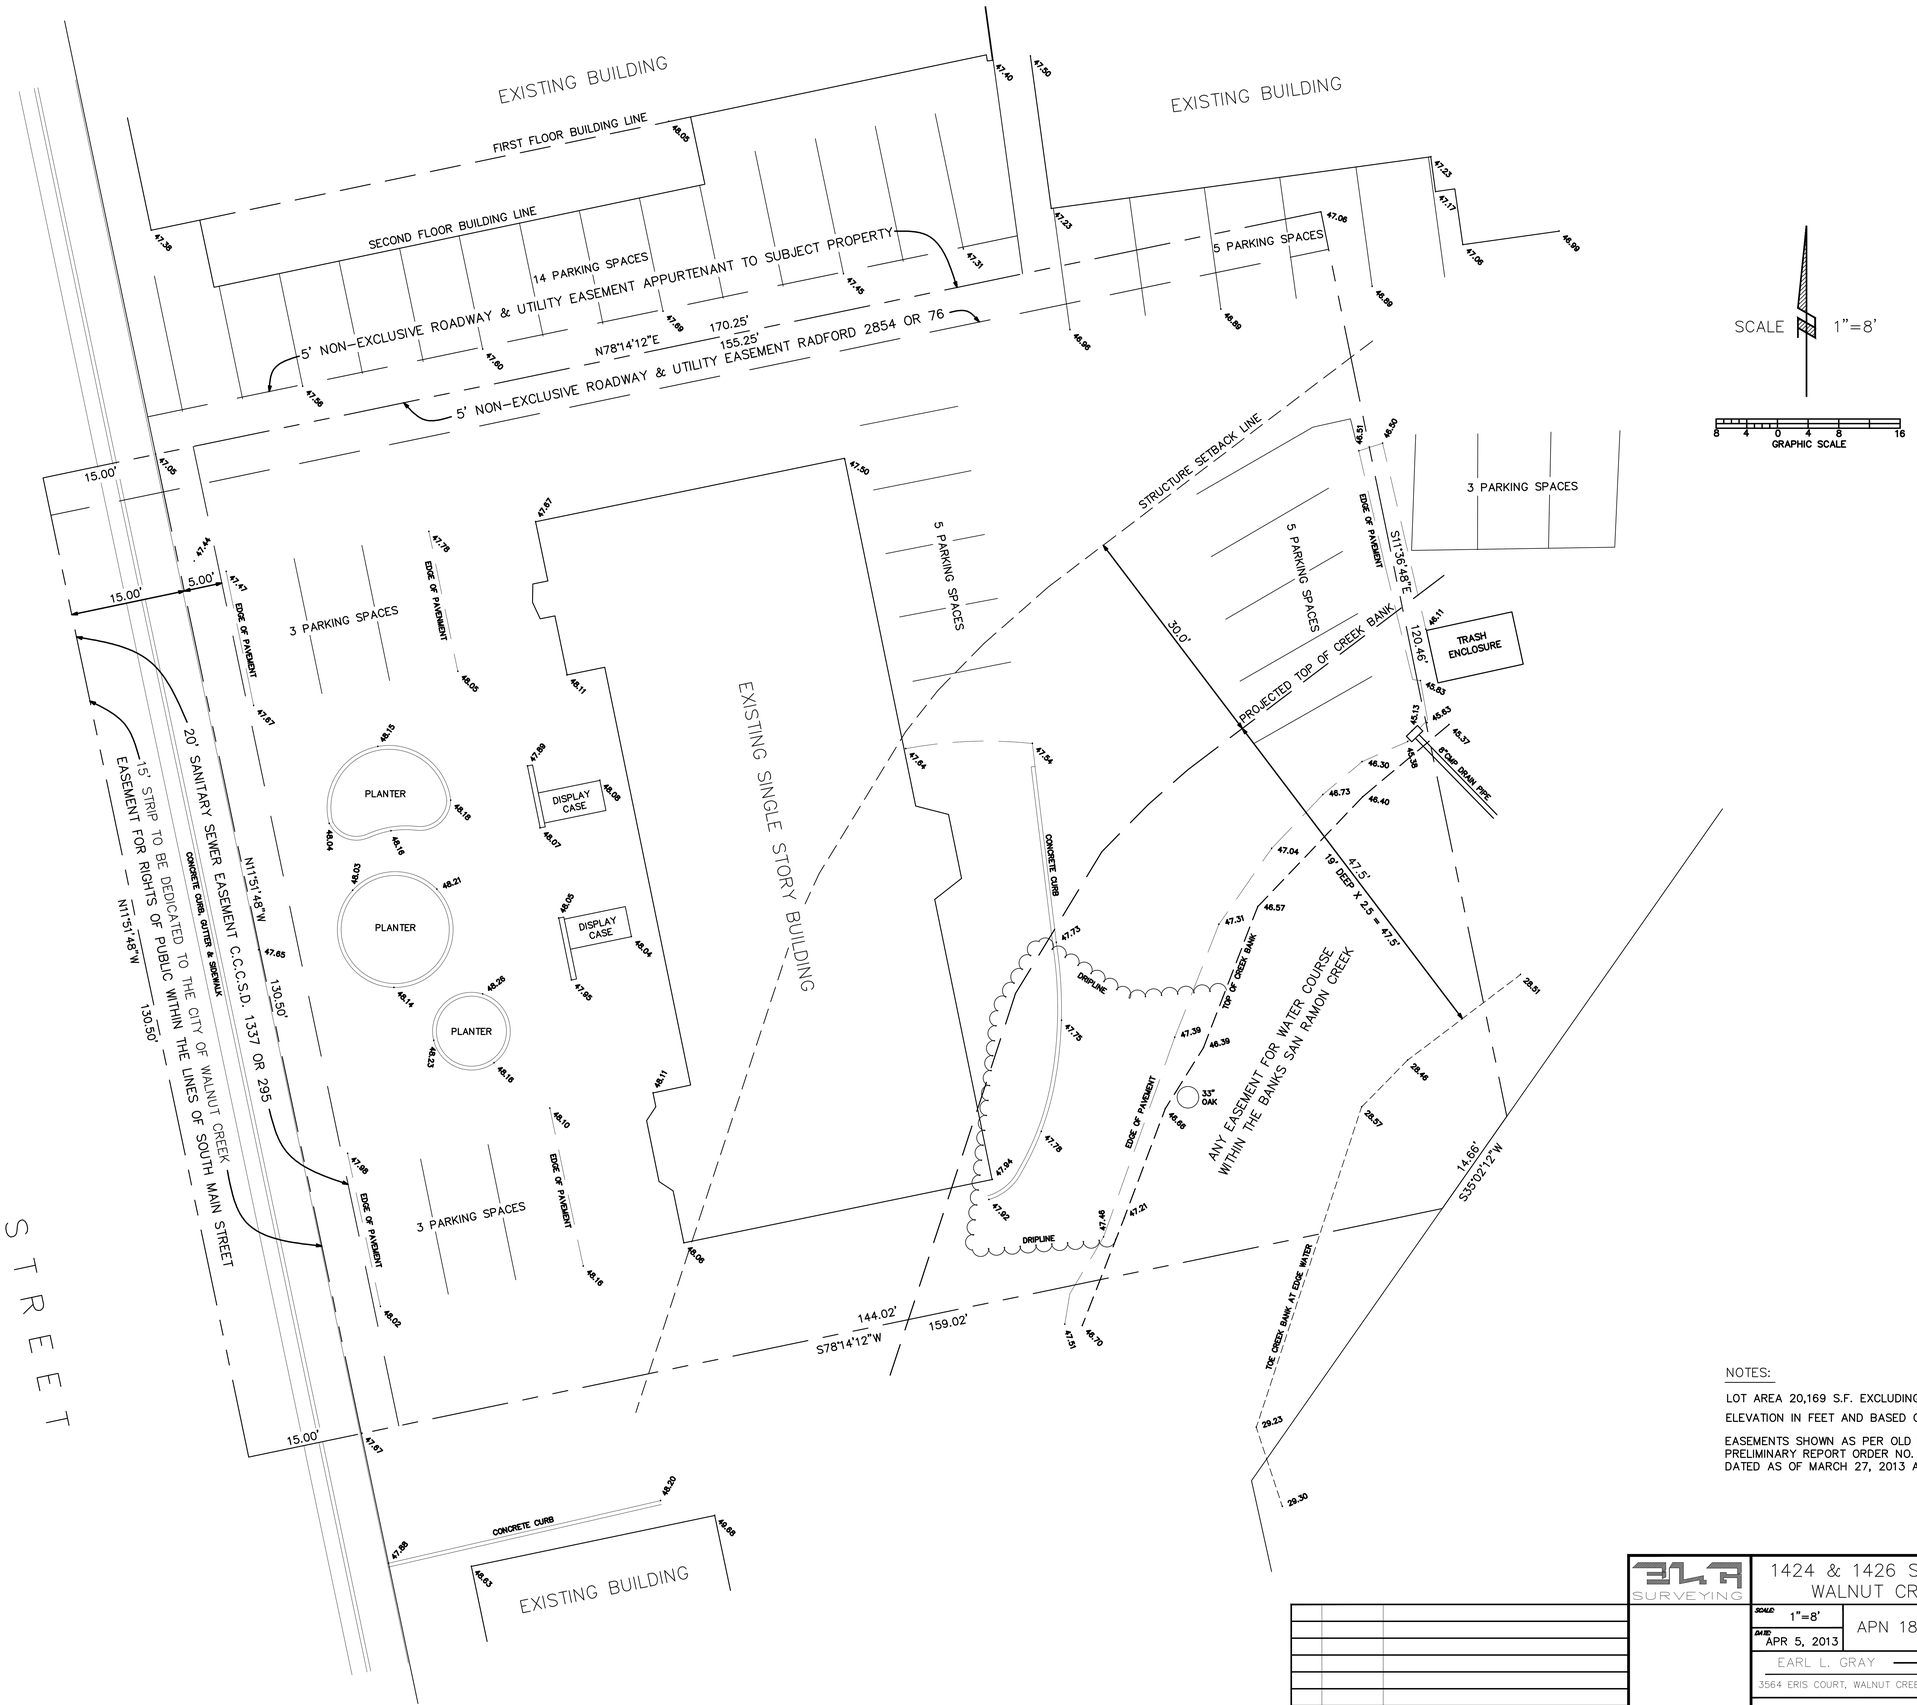


NOTES:

LOT AREA 20,169 S.F. EXCLUDING THE DEDICATION

ELEVATION IN FEET AND BASED ON AN ASSUMED DATUM

EASEMENTS SHOWN AS PER OLD REPUBLIC TITLE COMPANY PRELIMINARY REPORT ORDER NO. 0147012515-SH DATED AS OF MARCH 27, 2013 AT 7:30 AM

| No. | DATE | REVISIONS |
|---|---|---|
| 1 | 5-28-2013 | ADD PARKING SPACE AT REAR OF BUILDING |

ELA SURVEYING

1424 & 1426 SOUTH MAIN STREET
WALNUT CREEK, CALIFORNIA

SCALE 1"=8' | APN 183-030-005 | DRAWN ELG | CHECKED ELG

DATE APR 5, 2013

EARL L. GRAY — Licensed Land Surveyor

3564 ERIS COURT, WALNUT CREEK, CALIFORNIA, 94598 (925) 934-4322

LOCATION SURVEY | DWG. NO. 1318

LCA ARCHITECTS

WWW . LCA - ARCHITECTS . COM

CARL E. CAMPOS
DAVID BOOSTAD
PETER STACKPOLE

590 YGNACIO VALLEY ROAD, SUITE 310
WALNUT CREEK, CALIFORNIA 94596
(925) 944-1626

1970 BROADWAY, SUITE 800
OAKLAND, CALIFORNIA 94612
(510) 272-1060

# 1426 S. MAIN ST

RETAIL & RESIDENTIAL ADDITION

LCA ARCHITECTS
RESTRICTED ARCHITECTURAL DRAWINGS

THE INFORMATION, PLANS, DESIGNS, NOTES AND ARRANGEMENTS SHOWN ON THIS DRAWING ARE CONFIDENTIAL AND MAY NOT BE REPRODUCED IN WHOLE OR IN PART WITHOUT THE EXPRESSED WRITTEN PERMISSION OF LCA ARCHITECTS. DRAWINGS NOTED AS PRELIMINARY, SCHEMATIC AND / OR CONCEPT CONTAIN INFORMATION THAT IS CONCEPTUAL AND SUBJECT TO VERIFICATION AND/OR CHANGE. THE ARCHITECT MAKES NO CLAIM FOR ACCURACY OF CONCEPTUAL INFORMATION OR OF INFORMATION SUPPLIED BY OTHERS.

SURVEY

SCALE: AS NOTED
DATE: 06 / 19 / 2019

REVISIONS:

PROJECT NO. 13034

G1

SHEET OF

# 1426 S. MAIN ST

**RETAIL & RESIDENTIAL ADDITION**

**OPTION A - RETAIL ADDITION + 3 STUDIO LOFT APARTMENTS**

## PROJECT DATA:

ADDRESS
1426 S MAIN ST
WALNUT CREEK, CA 94596

APN
183-030-005

LOT SIZE
22,134 SF

BUILDING SIZE
EXISTING BUILDING: 3727 SF
PROPOSED ADDITION: 1792 SF
TOTAL: 5519 SF

LOT COVERAGE
EXISTING: 3727 / 22134 = 17%
PROPOSED: 5519 / 22134 = 25%

SETBACK CALCULATIONS:

REQUIRED:
25' AVG. SETBACK
25'x96' = 2400 SF REQUIRED

PROVIDED:
20' x 56' = 1120 SF
20' x 47' = 940 SF
20' x 47' = 940 SF
TOTAL: 3000 SF

PARKING REQUIRED
1 SPACE/250 SF OF RENTABLE RETAIL SPACE:

EXISTING: 3727 SF


PROPOSED: 1792 SF (ADDITION) + 3727 SF = 5519 SF

PARKING REQUIRED: 22 STALLS

3 STUDIO APARTMENTS x 1.25 STALLS/STUDIO = 3.75


TOTAL STALLS REQUIRED: 26

TOTAL STALLS PROVIDED: 24

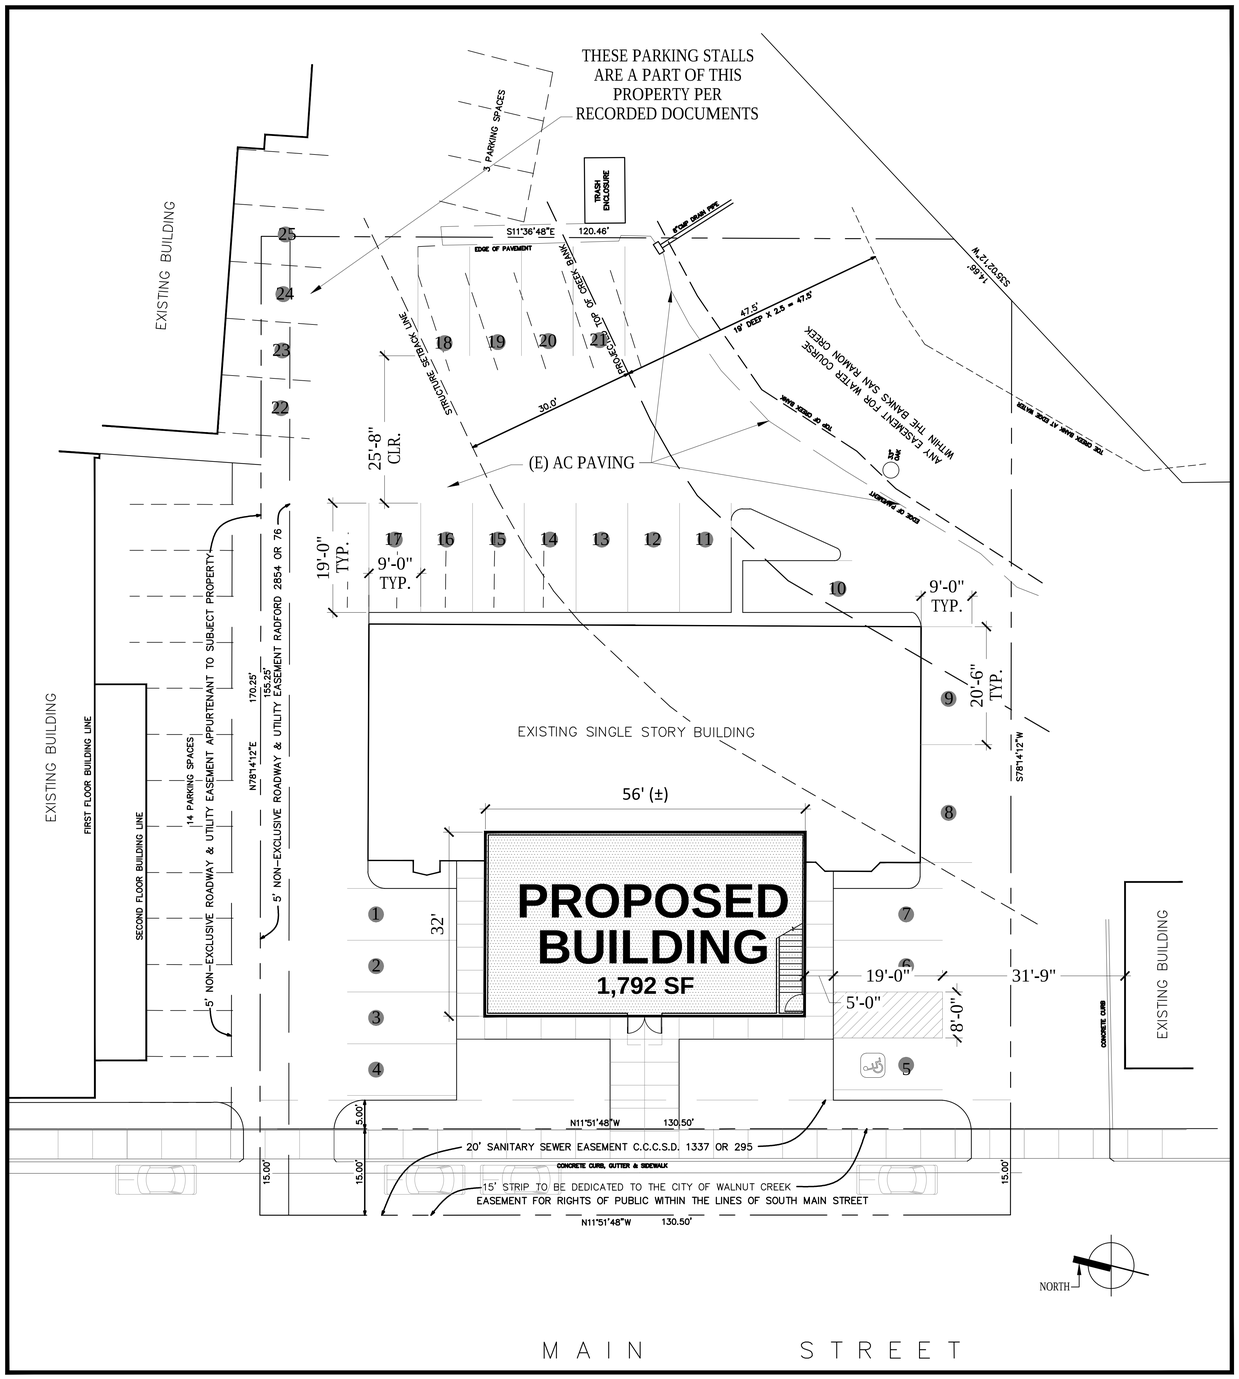


## 1 SITE PLAN

SCALE: 3/32" = 1'-0"

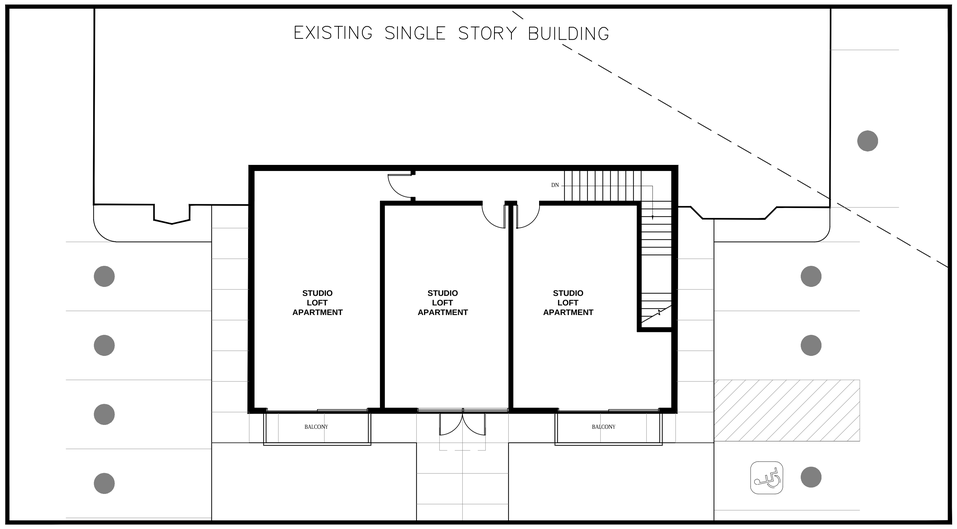


## 2 2nd STORY APARTMENT PLAN

SCALE: 1/8" = 1'-0"




## 3 ELEVATION

SCALE: 1/8" = 1'-0"

8' 0' 8' 16'
SCALE: 1/8" = 1'-0"

10'-8" 0' 10'-8" 21'-4"
SCALE: 1/32" = 1'-0"


LCA ARCHITECTS

WWW . LCA - ARCHITECTS . COM

CARL E. CAMPOS
DAVID ROGSTAD
PETER STACKPOLE

590 YGNACIO VALLEY ROAD, SUITE 310
WALNUT CREEK, CALIFORNIA 94596
(925) 944-1626

1970 BROADWAY, SUITE 800
OAKLAND, CALIFORNIA 94612
(510) 272-1060


1426 S. MAIN ST
RETAIL & RESIDENTIAL ADDITION


LCA ARCHITECTS
RESTRICTED ARCHITECTURAL DRAWINGS

THE INFORMATION, PLANS, DESIGNS, NOTES AND ARRANGEMENTS SHOWN ON THIS DRAWING ARE CONFIDENTIAL AND MAY NOT BE REPRODUCED IN WHOLE OR IN PART WITHOUT THE EXPRESSED WRITTEN PERMISSION OF LCA ARCHITECTS.
DRAWINGS NOTED AS PRELIMINARY OR SIMILAR DOES NOT CONTAIN INFORMATION THAT IS CONCEPTUAL AND SUBJECT TO VERIFICATION AND/OR CHANGE. THE ARCHITECT MAKES NO CLAIM FOR ACCURACY OF CONCEPTUAL INFORMATION OR OF INFORMATION SUPPLIED BY OTHERS.


SCHEME A:
SITE PLAN
2ND FLOOR PLAN
ELEVATION

SCALE: AS NOTED
DATE: 06 / 19 / 2019

REVISIONS:

PROJECT NO. 13034

**A1**

SHEET OF

# 1426 S. MAIN ST

**RETAIL & RESIDENTIAL ADDITION**
**OPTION B - RETAIL ADDITION + 3 STUDIO LOFT APARTMENTS + 2 ONE-BEDROOM LOFT APARTMENTS**

## PROJECT DATA:

ADDRESS
1426 S MAIN ST
WALNUT CREEK, CA 94596

APN
183-030-005

LOT SIZE
22,134 SF

BUILDING SIZE
EXISTING BUILDING: 3727 SF
PROPOSED ADDITION: 2592 SF
TOTAL: 6319 SF

LOT COVERAGE
EXISTING: 3727/22134 = 17%
PROPOSED: 6319/22134 = 29%

SETBACK CALCULATIONS:
REQUIRED:
25' AVG. SETBACK
25'x96' = 2400 SF REQUIRED

PROVIDED:
5' x 56' = 280 SF
20' x 47' = 940 SF
20' x 47' = 940 SF
TOTAL: 2120 SF

PARKING REQUIRED
1 SPACE/250 SF OF RETAIL:

EXISTING: 3727 SF


PROPOSED: 2592 SF (ADDITION) + 3727 SF = 6319 SF

PARKING REQUIRED: 25 STALLS

3 STUDIO APARTMENTS x 1.25 STALLS = 3.75
2 ONE-BEDROOM x 1.5 STALLS = 3


TOTAL STALLS REQUIRED: 32

TOTAL STALLS PROVIDED: 25

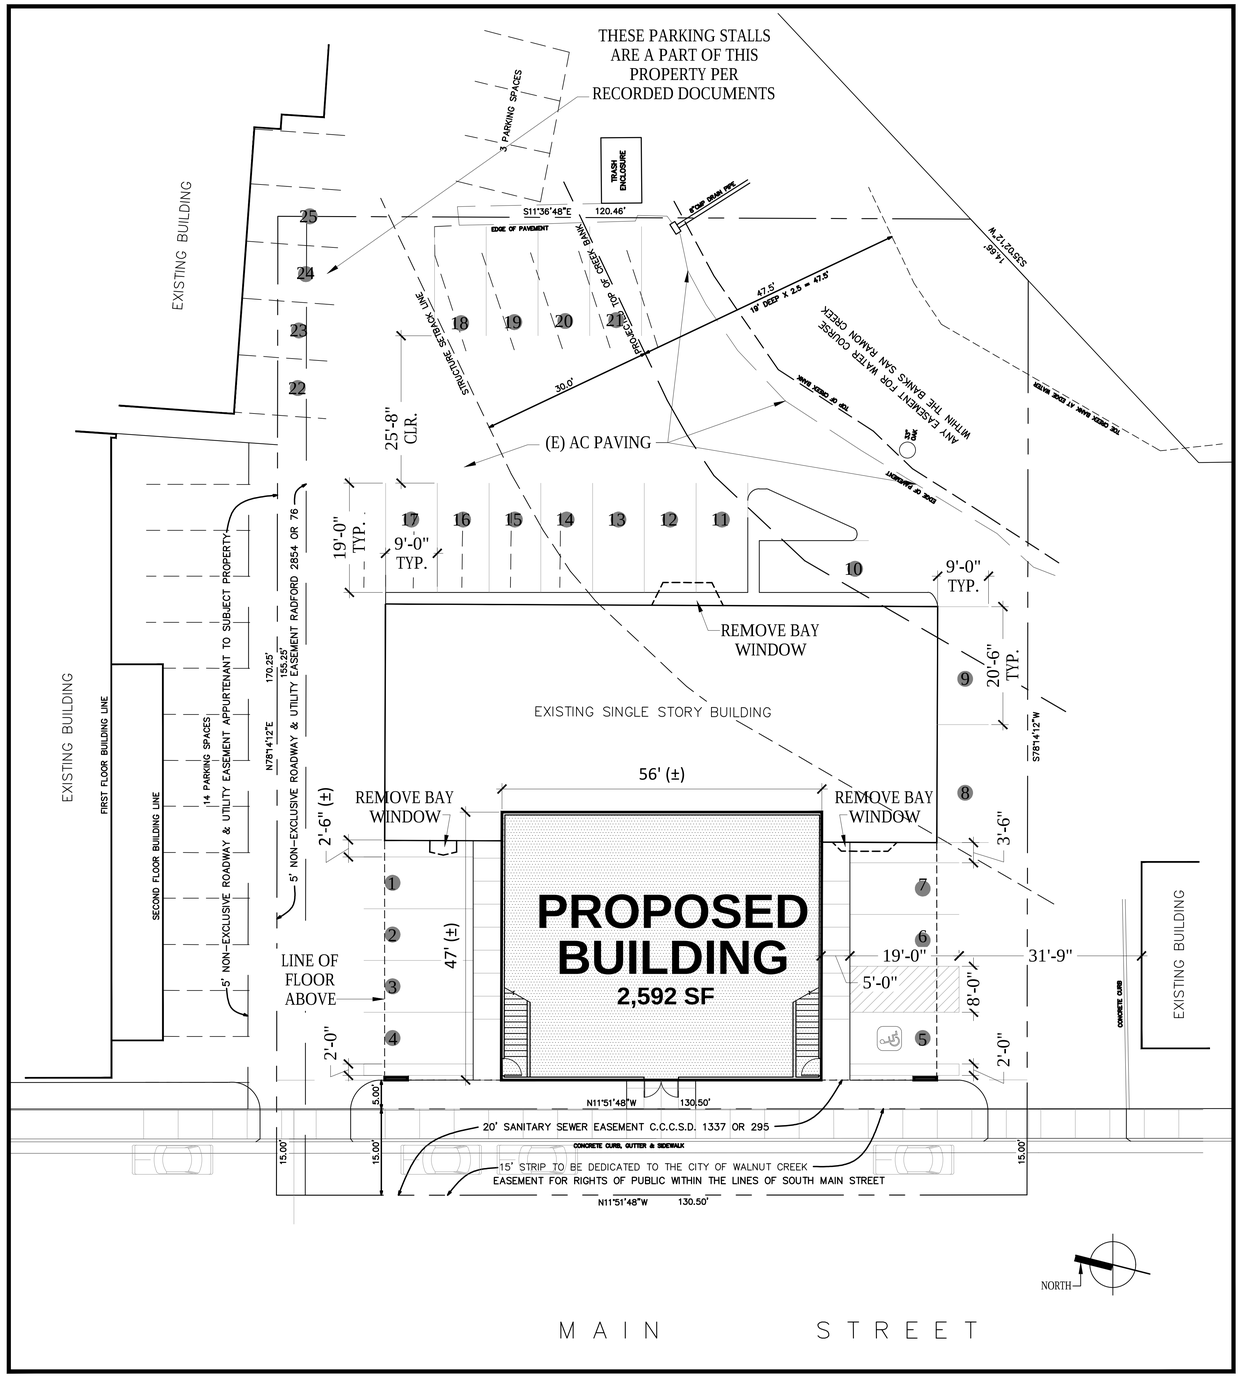


## 1 SITE PLAN

SCALE: 3/32" = 1'-0"

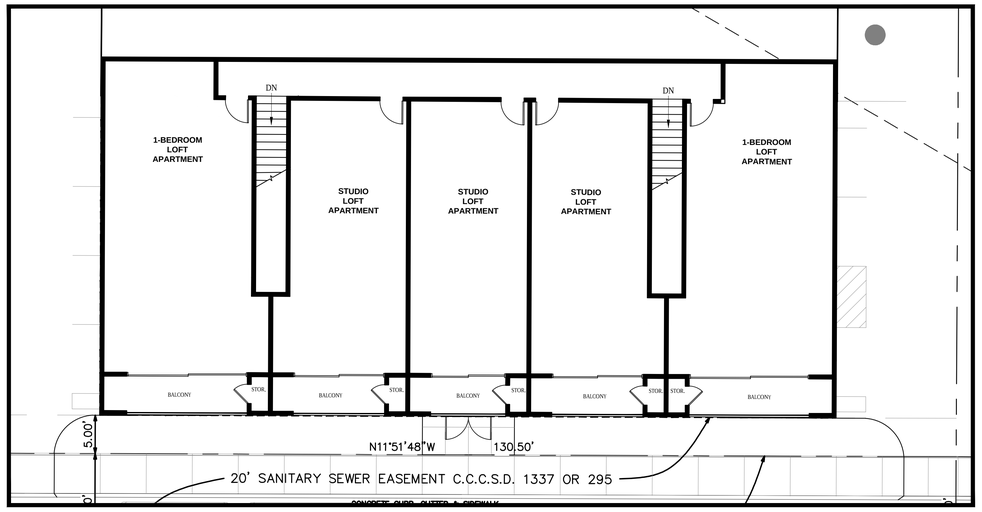


## 2 2nd STORY APARTMENT PLAN

SCALE: 1/8" = 1'-0"




## 3 ELEVATION

SCALE: 1/8" = 1'-0"

8' 0' 8' 16'
SCALE: 1/8" = 1'-0"

10'-8" 0' 10'-8" 21'-4"
SCALE: 1/32" = 1'-0"

LCA ARCHITECTS


WWW . LCA - ARCHITECTS . COM

CARL E. CAMPOS
DAVID BOGSTAD
PETER STACKPOLE

590 YGNACIO VALLEY ROAD, SUITE 310
WALNUT CREEK, CALIFORNIA 94596
(925) 944-1626

1970 BROADWAY, SUITE 800
OAKLAND, CALIFORNIA 94612
(510) 272-1060


1426 S. MAIN ST
RETAIL & RESIDENTIAL ADDITION


LCA ARCHITECTS
RESTRICTED ARCHITECTURAL DRAWINGS

THE INFORMATION, PLANS, DESIGNS, NOTES AND ARRANGEMENTS SHOWN ON THIS DRAWING ARE CONFIDENTIAL AND MAY NOT BE REPRODUCED IN WHOLE OR IN PART WITHOUT THE EXPRESSED WRITTEN PERMISSION OF LCA ARCHITECTS. DRAWINGS NOTED AS PRELIMINARY, SCHEMATIC AND / OR CONCEPT CONTAIN INFORMATION THAT IS CONCEPTUAL AND SUBJECT TO VERIFICATION AND/OR CHANGE. THE ARCHITECT MAKES NO CLAIM FOR ACCURACY OF CONCEPTUAL INFORMATION OR OF INFORMATION SUPPLIED BY OTHERS.


SCHEME B:
SITE PLAN
2ND LEVEL PLAN
ELEVATION

SCALE: AS NOTED
DATE: 06 / 19 / 2019

REVISIONS:

PROJECT NO. 13034

**A2**

SHEET OF

# 1426 S. MAIN ST

**RETAIL & RESIDENTIAL ADDITION**
**OPTION C - RETAIL ADDITION + 3 STUDIO LOFT APARTMENTS + 2 ONE-BEDROOM LOFT APARTMENTS**

## PROJECT DATA:

ADDRESS
1426 S MAIN ST
WALNUT CREEK, CA 94596

APN
183-030-005

LOT SIZE
22,134 SF

BUILDING SIZE
EXISTING BUILDING: 3727 SF
PROPOSED ADDITION: 3216 SF
TOTAL: 6943 SF

LOT COVERAGE
EXISTING: 3727 / 22134 = 17%
PROPOSED: 6943 / 22134 = 31%

SETBACK CALCULATIONS:
REQUIRED:
25' AVG. SETBACK
25'x96' = 2400 SF REQUIRED

PROVIDED:
5' x 56' = 280 SF
20' x 47' = 940 SF
TOTAL: 1180 SF

PARKING REQUIRED
1 SPACE/250 SF OF RETAIL:

EXISTING: 3727 SF


PROPOSED: 3216 SF (ADDITION) + 3727 SF = 6943 SF

PARKING REQUIRED: 28 STALLS

3 STUDIO APARTMENTS x 1.25 STALLS = 3.75
2 ONE-BEDROOM x 1.5 STALLS = 3


TOTAL STALLS REQUIRED: 35

TOTAL STALLS PROVIDED: 23

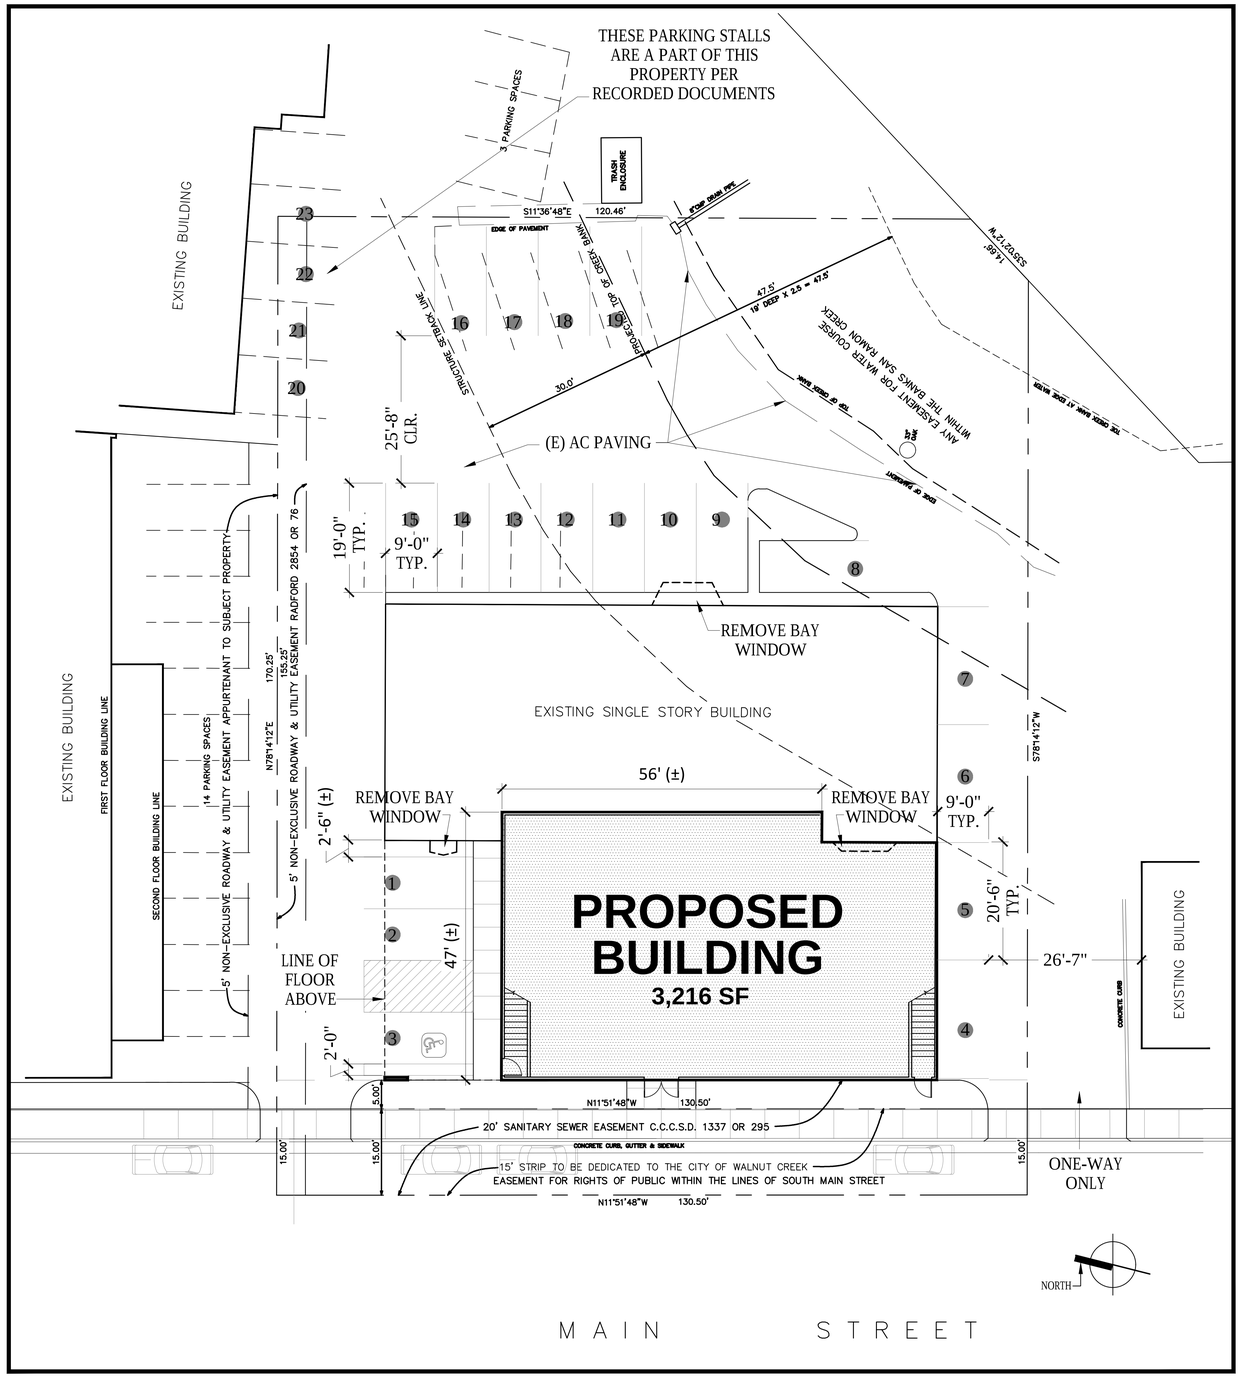


## 1 SITE PLAN

SCALE: 3/32" = 1'-0"

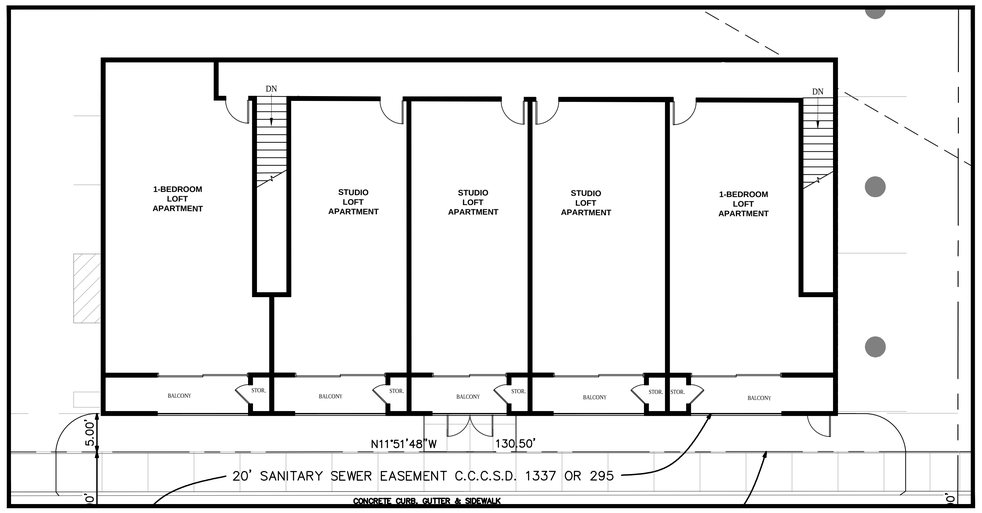


## 2 2nd STORY APARTMENT PLAN

SCALE: 1/8" = 1'-0"




## 3 ELEVATION

SCALE: 1/8" = 1'-0"

8' 0' 8' 16'
SCALE: 1/8" = 1'-0"

10'-8" 0' 10'-8" 21'-4"
SCALE: 1/32" = 1'-0"

LCA ARCHITECTS
WWW . LCA - ARCHITECTS . COM
CARL E. CAMPOS
DAVID BOGSTAD
PETER STACKPOLE
590 YGNACIO VALLEY ROAD, SUITE 310
WALNUT CREEK, CALIFORNIA 94596
(925) 944-1626
1970 BROADWAY, SUITE 800
OAKLAND, CALIFORNIA 94612
(510) 272-1060

1426 S. MAIN ST
RETAIL & RESIDENTIAL ADDITION

LCA ARCHITECTS
RESTRICTED ARCHITECTURAL DRAWINGS
THE INFORMATION, PLANS, DESIGNS, NOTES AND ARRANGEMENTS SHOWN ON THIS DRAWING ARE CONFIDENTIAL AND MAY NOT BE REPRODUCED IN WHOLE OR IN PART WITHOUT THE EXPRESSED WRITTEN PERMISSION OF LCA ARCHITECTS. DRAWINGS NOTED AS PRELIMINARY, SCHEMATIC AND / OR CONCEPT CONTAIN INFORMATION THAT IS CONCEPTUAL AND SUBJECT TO VERIFICATION AND/OR CHANGE. THE ARCHITECT MAKES NO CLAIM FOR ACCURACY OF CONCEPTUAL INFORMATION OR OF INFORMATION SUPPLIED BY OTHERS.

SCHEME C:
SITE PLAN
2ND LEVEL PLAN
ELEVATION

SCALE: AS NOTED
DATE: 06 / 19 / 2019

REVISIONS:

PROJECT NO. 13034

A3

SHEET OF