

1 PERSPECTIVE VIEW



2 VINCITY MAP

1426 S. MAIN ST

RETAIL & RESIDENTIAL ADDITION

SHEET INDEX

G0 COVER SHEET, PERSPECTIVE VIEW AND VICINITY MAP
G1 SURVEY
A1 SITE PLAN
A2 ELEVATION AND RESIDENTIAL FLOOR PLAN
A3 CONCEPTUAL COLOR & MATERIAL BOARD

LCA ARCHITECTS

WWW . LCA - ARCHITECTS . COM

CARL E. CAMPOS
DAVID BOGSTAD
PETER STACKPOLE

590 YGNACIO VALLEY ROAD, SUITE 310
WALNUT CREEK, CALIFORNIA 94596
(925) 944-1626

1970 BROADWAY, SUITE 800
OAKLAND, CALIFORNIA 94612
(510) 272-1060

1426 S. MAIN ST
RETAIL & RESIDENTIAL ADDITION

LCA ARCHITECTS
RESTRICTED ARCHITECTURAL DRAWINGS

THE INFORMATION, PLANS, DESIGNS, NOTES AND ARRANGEMENTS SHOWN ON THIS DRAWING ARE CONFIDENTIAL AND MAY NOT BE REPRODUCED IN WHOLE OR IN PART WITHOUT THE EXPRESSED WRITTEN PERMISSION OF LCA ARCHITECTS. DRAWINGS NOTED AS PRELIMINARY, SCHEMATIC AND / OR CONCEPT CONTAIN INFORMATION THAT IS CONCEPTUAL AND SUBJECT TO VERIFICATION AND/OR CHANGE. THE ARCHITECT MAKES NO CLAIM FOR ACCURACY OF CONCEPTUAL INFORMATION OR OF INFORMATION SUPPLIED BY OTHERS.

COVER SHEET
PERSPECTIVE VIEW
VICINITY MAP


SCALE:
DATE: 10 / 08 / 19

REVISIONS:

PROJECT NO. 13034

G0

SHEET OF

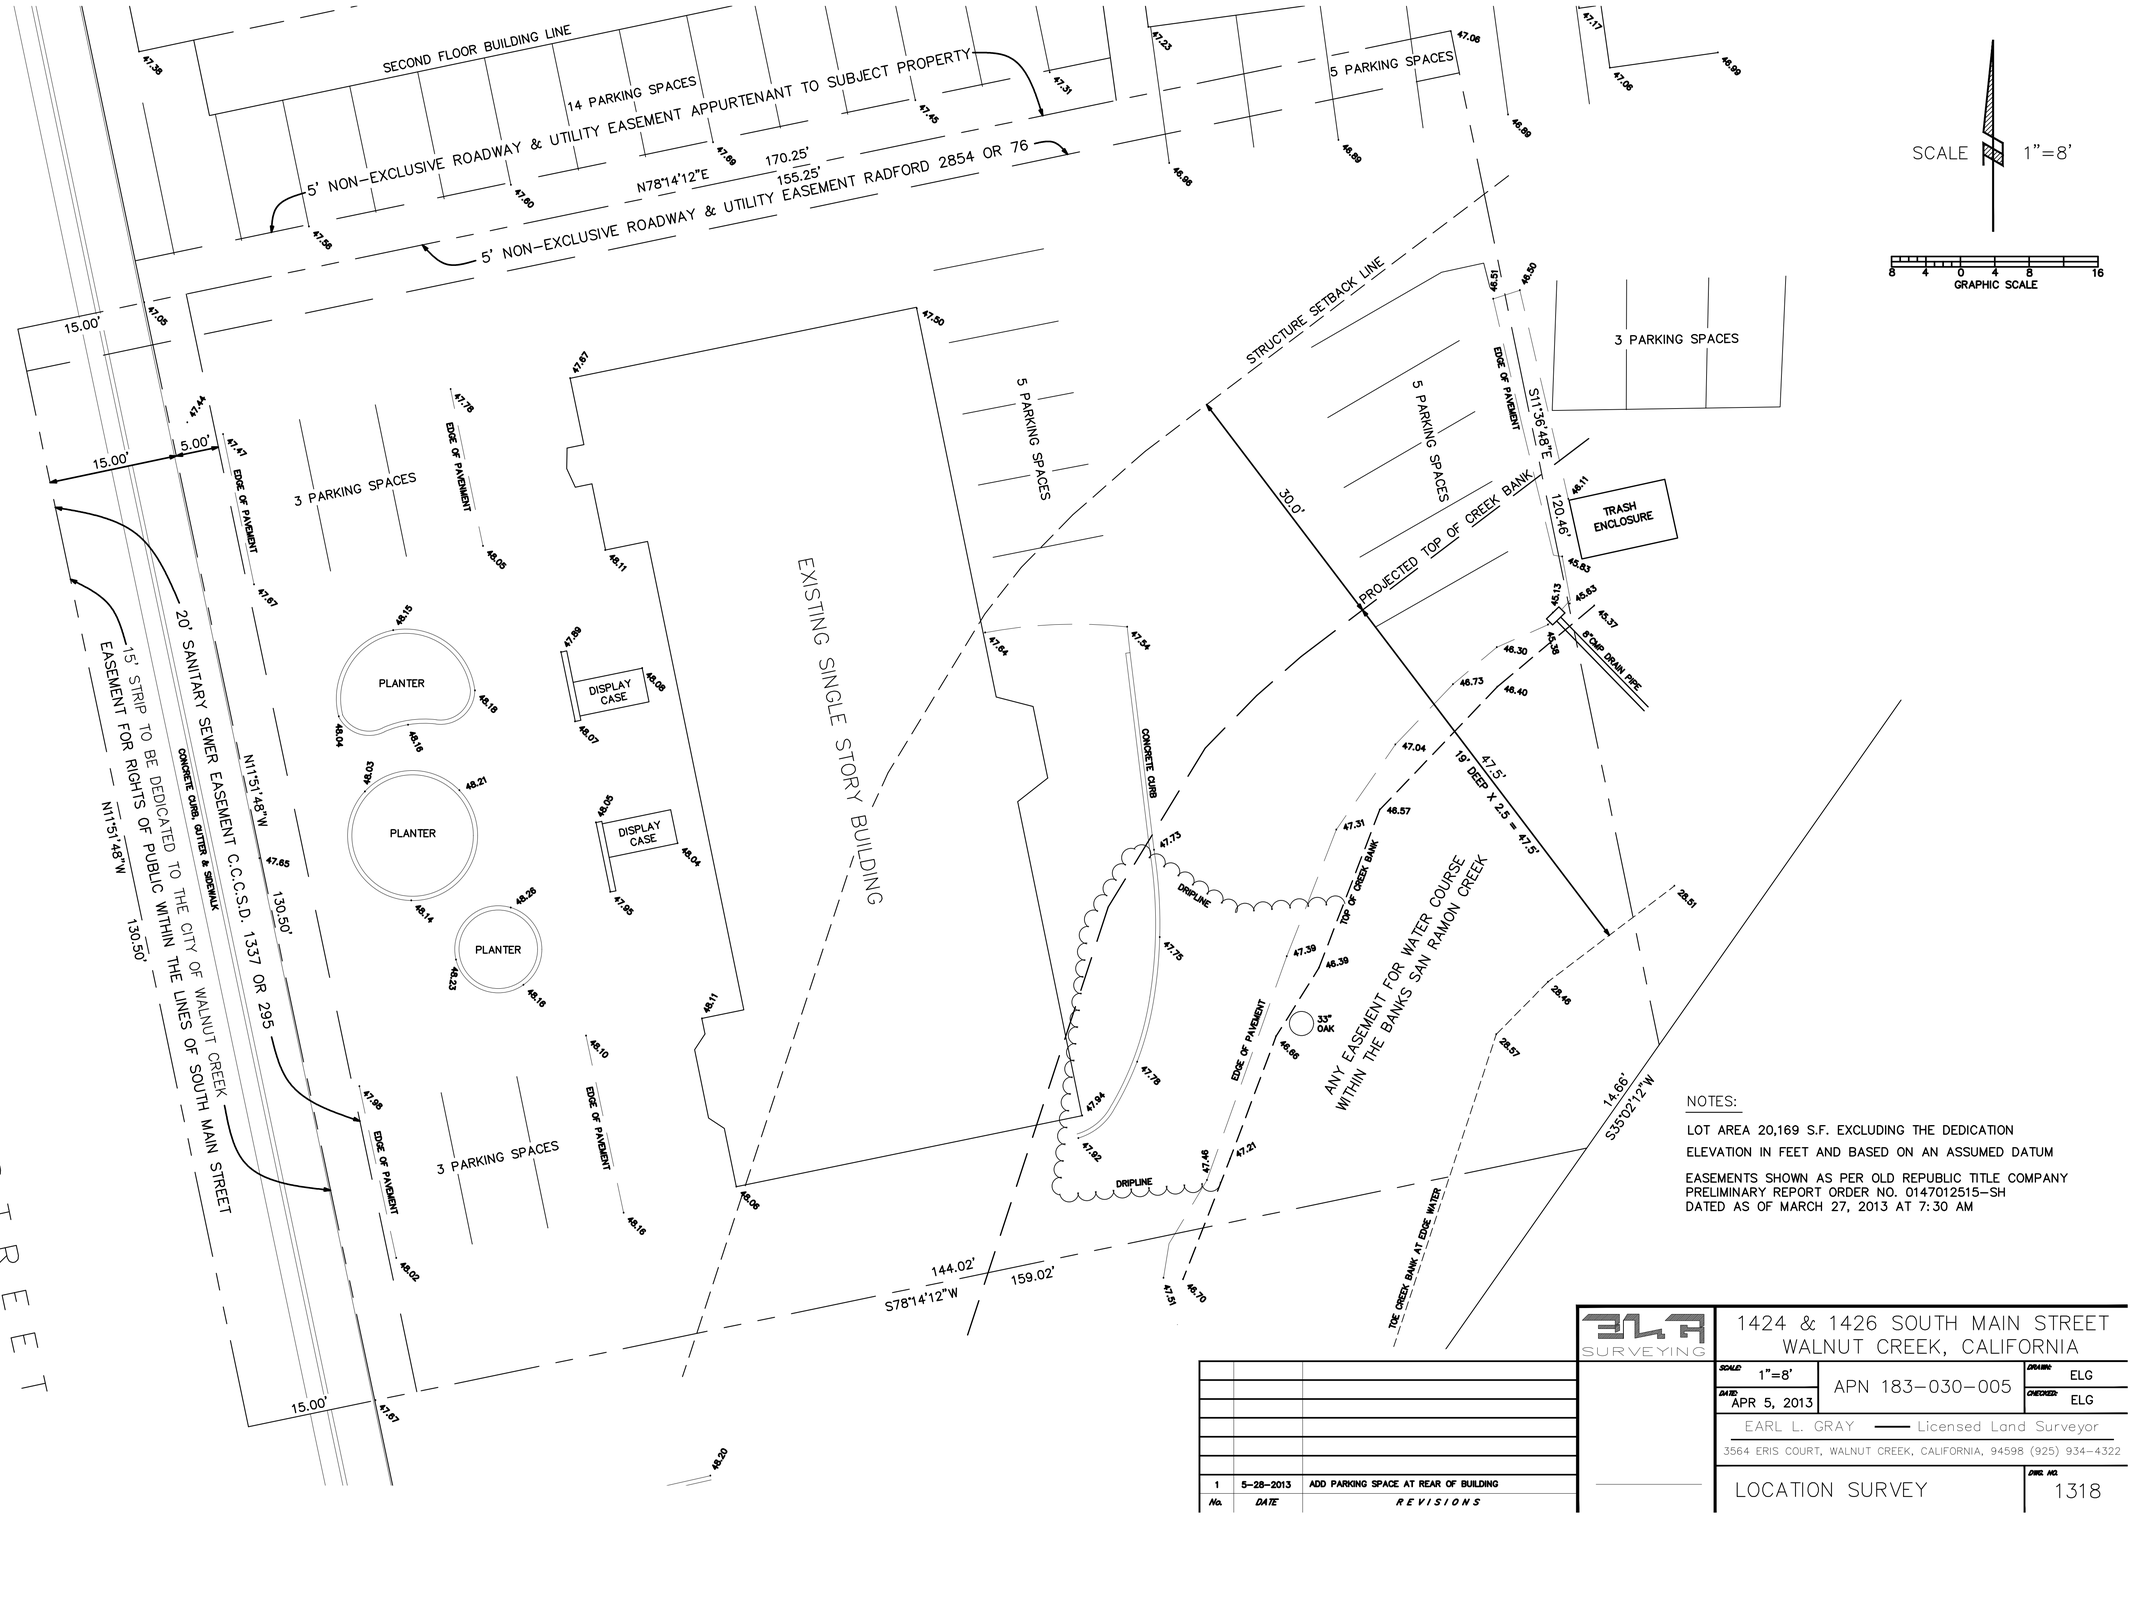

NOTES:

LOT AREA 20,169 S.F. EXCLUDING THE DEDICATION

ELEVATION IN FEET AND BASED ON AN ASSUMED DATUM

EASEMENTS SHOWN AS PER OLD REPUBLIC TITLE COMPANY PRELIMINARY REPORT ORDER NO. 0147012515-SH DATED AS OF MARCH 27, 2013 AT 7:30 AM

No.	DATE	REVISIONS
1	5-28-2013	ADD PARKING SPACE AT REAR OF BUILDING

ELG SURVEYING

1424 & 1426 SOUTH MAIN STREET
WALNUT CREEK, CALIFORNIA

SCALE: 1"=8' | APN 183-030-005 | DRAWN: ELG
DATE: APR 5, 2013 | CHECKED: ELG

EARL L. GRAY — Licensed Land Surveyor
3564 ERIS COURT, WALNUT CREEK, CALIFORNIA, 94598 (925) 934-4322

LOCATION SURVEY | DWG. NO. 1318

LCA ARCHITECTS

WWW . LCA - ARCHITECTS . COM

CARL E. CAMPOS
DAVID BOGSTAD
PETER STACKPOLE

590 YGNACIO VALLEY ROAD, SUITE 310
WALNUT CREEK, CALIFORNIA 94596
(925) 944-1626

1970 BROADWAY, SUITE 800
OAKLAND, CALIFORNIA 94612
(510) 272-1060

1426 S. MAIN ST

RETAIL & RESIDENTIAL ADDITION

LCA ARCHITECTS
RESTRICTED ARCHITECTURAL DRAWINGS

THE INFORMATION, PLANS, DESIGNS, NOTES AND ARRANGEMENTS SHOWN ON THIS DRAWING ARE CONFIDENTIAL AND MAY NOT BE REPRODUCED IN WHOLE OR IN PART WITHOUT THE EXPRESSED WRITTEN PERMISSION OF LCA ARCHITECTS. DRAWINGS NOTED AS PRELIMINARY, SCHEMATIC AND / OR CONCEPT CONTAIN INFORMATION THAT IS CONCEPTUAL AND SUBJECT TO VERIFICATION AND/OR CHANGE. THE ARCHITECT MAKES NO CLAIM FOR ACCURACY OF CONCEPTUAL INFORMATION OR OF INFORMATION SUPPLIED BY OTHERS.

SURVEY

SCALE: AS NOTED
DATE: 10 / 08 / 19

REVISIONS:

PROJECT NO. 13034

G1

SHEET OF

1426 S. MAIN ST

RETAIL & RESIDENTIAL ADDITION

RETAIL ADDITION + 3 STUDIO LOFT APARTMENTS + 2 ONE-BEDROOM LOFT APARTMENTS

PROJECT DATA:

ADDRESS
1426 S MAIN ST
WALNUT CREEK, CA 94596

APN
183-030-005

LOT SIZE
22,134 SF

BUILDING SIZE

EXISTING BUILDING:	3727 SF
PROPOSED ADDITION:	3216 SF
TOTAL:	6943 SF

LOT COVERAGE

EXISTING:	3727 / 22134 = 17%
PROPOSED:	6943 / 22134 = 31%

SETBACK CALCULATIONS:

REQUIRED:
25' AVG. SETBACK
25'x96' = 2400 SF REQUIRED

PROVIDED:
5' x 56' = 280 SF
20' x 47' = 940 SF
TOTAL: 1180 SF

PARKING REQUIRED
1 SPACE/250 SF OF RETAIL:

EXISTING: 3727 SF


PROPOSED: 3216 SF (ADDITION) + 3727 SF = 6943 SF

PARKING REQUIRED: 28 STALLS

3 STUDIO APARTMENTS x 1.25 STALLS = 3.75
2 ONE-BEDROOM x 1.5 STALLS = 3

TOTAL STALLS REQUIRED: 35

TOTAL STALLS PROVIDED: 23

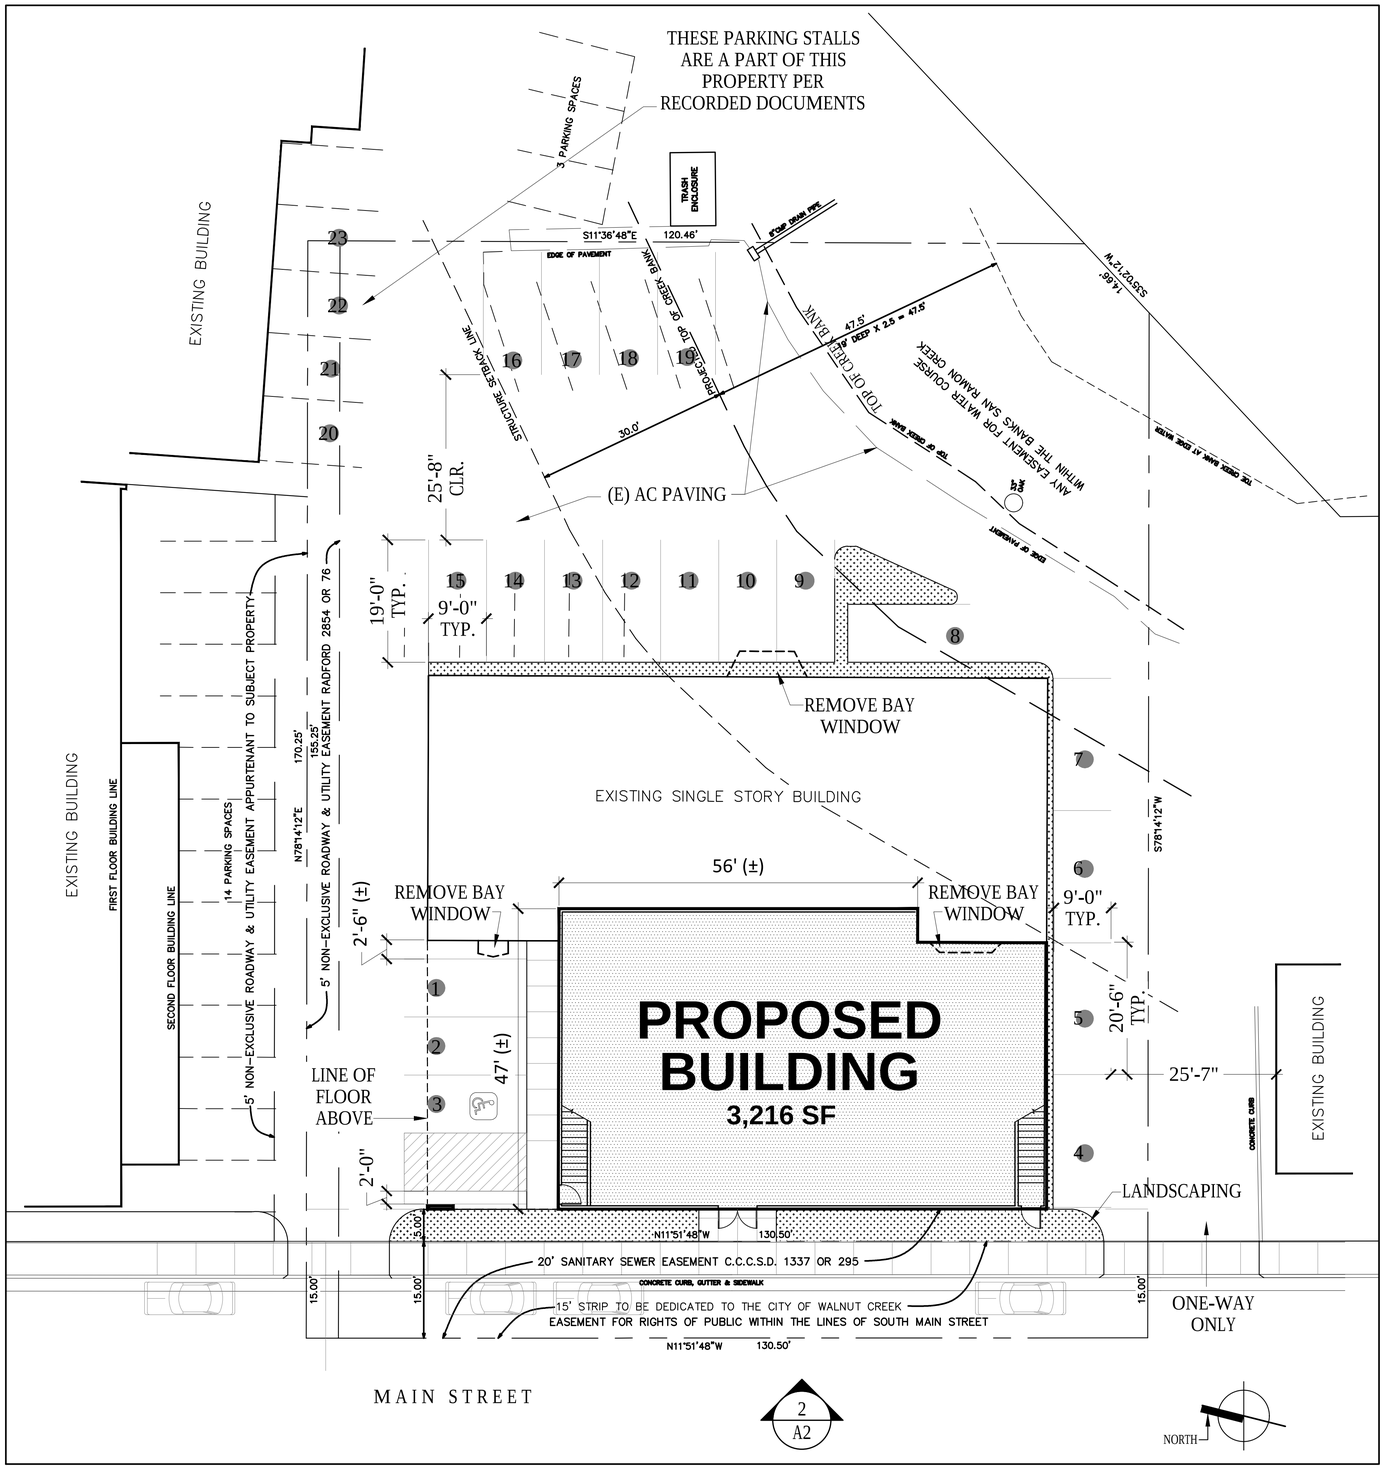

1 SITE PLAN

SCALE: 3/32" = 1'-0"

10'-8" 0' 10'-8" 21'-4"
SCALE: 3/32" = 1'-0"

LCA ARCHITECTS

WWW . LCA - ARCHITECTS . COM

CARL E. CAMPOS
DAVID BOGSTAD
PETER STACKPOLE

590 YGNACIO VALLEY ROAD, SUITE 310
WALNUT CREEK, CALIFORNIA 94596
(925) 944-1626

1970 BROADWAY, SUITE 800
OAKLAND, CALIFORNIA 94612
(510) 272-1060

1426 S. MAIN ST
RETAIL & RESIDENTIAL ADDITION

LCA ARCHITECTS
RESTRICTED ARCHITECTURAL DRAWINGS

THE INFORMATION, PLANS, DESIGNS, NOTES AND ARRANGEMENTS SHOWN ON THIS DRAWING ARE CONFIDENTIAL AND MAY NOT BE REPRODUCED IN WHOLE OR IN PART WITHOUT THE EXPRESSED WRITTEN PERMISSION OF LCA ARCHITECTS. DRAWINGS NOTED AS PRELIMINARY, SCHEMATIC AND / OR CONCEPT CONTAIN INFORMATION THAT IS CONCEPTUAL AND SUBJECT TO VERIFICATION AND/OR CHANGE. THE ARCHITECT MAKES NO CLAIM FOR ACCURACY OF CONCEPTUAL INFORMATION OR OF INFORMATION SUPPLIED BY OTHERS.

SITE PLAN


SCALE: AS NOTED
DATE: 10 / 08 / 19

REVISIONS:

PROJECT NO. 13034

A1

SHEET OF

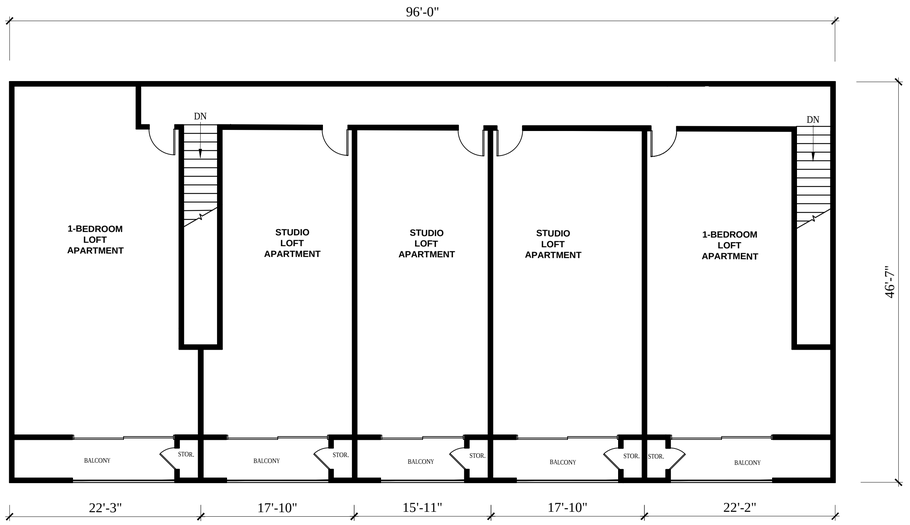

1 2nd STORY APARTMENT PLAN

SCALE: 1/8" = 1'-0"



2 ELEVATION

SCALE: 1/8" = 1'-0"

8' 0' 8' 16'

SCALE: 1/8" = 1'-0"

LCA ARCHITECTS

WWW . LCA - ARCHITECTS . COM

CARL E. CAMPOS
DAVID BOGSTAD
PETER STACKPOLE

590 YGNACIO VALLEY ROAD, SUITE 310
WALNUT CREEK, CALIFORNIA 94596
(925) 944-1626

1970 BROADWAY, SUITE 800
OAKLAND, CALIFORNIA 94612
(510) 272-1060

1426 S. MAIN ST

RETAIL & RESIDENTIAL ADDITION

LCA ARCHITECTS
RESTRICTED ARCHITECTURAL DRAWINGS

THE INFORMATION, PLANS, DESIGNS, NOTES AND ARRANGEMENTS SHOWN ON THIS DRAWING ARE CONFIDENTIAL AND MAY NOT BE REPRODUCED IN WHOLE OR IN PART WITHOUT THE EXPRESSED WRITTEN PERMISSION OF LCA ARCHITECTS. DRAWINGS NOTED AS PRELIMINARY, SCHEMATIC AND / OR CONCEPT CONTAIN INFORMATION THAT IS CONCEPTUAL AND SUBJECT TO VERIFICATION AND/OR CHANGE. THE ARCHITECT MAKES NO CLAIM FOR ACCURACY OF CONCEPTUAL INFORMATION OR OF INFORMATION SUPPLIED BY OTHERS.

2ND LEVEL PLAN
ELEVATION

SCALE: AS NOTED
DATE: 10 / 08 / 19

REVISIONS:

PROJECT NO. 13034

A2

SHEET OF

KELLY MOORE
FASCIA
"ALUMINUM
SKY"
KM5820

KELLY MOORE
WINDOW &
DOOR FRAMES
"CARBON"
407

KELLY MOORE
BODY
"ANTIQUE
WHITE"
KM49



STAND ALONE
METAL LETTERS



EXTERIOR
WALL SCONCE



METAL GUARD
RAILING



CANOPY
ATTACHMENT

EQUIPMENT SCREEN

35’ HEIGHT LIMIT

ADIBS PERSIAN RUG CO.

1 FRONT ELEVATION

LCA ARCHITECTS

WWW . LCA - ARCHITECTS . COM

CARL E. CAMPOS
DAVID BOGSTAD
PETER STACKPOLE

590 YGNACIO VALLEY ROAD, SUITE 310
WALNUT CREEK, CALIFORNIA 94596
(925) 944-1626

1970 BROADWAY, SUITE 800
OAKLAND, CALIFORNIA 94612
(510) 272-1060

1426 S. MAIN ST

RETAIL & RESIDENTIAL ADDITION

LCA ARCHITECTS
RESTRICTED ARCHITECTURAL DRAWINGS

THE INFORMATION, PLANS, DESIGNS, NOTES AND ARRANGEMENTS SHOWN ON THIS DRAWING ARE CONFIDENTIAL AND MAY NOT BE REPRODUCED IN WHOLE OR IN PART WITHOUT THE EXPRESSED WRITTEN PERMISSION OF LCA ARCHITECTS. DRAWINGS NOTED AS PRELIMINARY, SCHEMATIC AND / OR CONCEPT CONTAIN INFORMATION THAT IS CONCEPTUAL AND SUBJECT TO VERIFICATION AND/OR CHANGE. THE ARCHITECT MAKES NO CLAIM FOR ACCURACY OF CONCEPTUAL INFORMATION OR OF INFORMATION SUPPLIED BY OTHERS.

COLOR AND
MATERIALS

SCALE: AS NOTED
DATE: 10 / 08 / 19

REVISIONS:

PROJECT NO. 13034

A3

SHEET OF