1426 S. MAIN ST

RETAIL & RESIDENTIAL ADDITION

RETAIL ADDITION + 3 STUDIO LOFT APARTMENTS + 2 ONE-BEDROOM LOFT APARTMENTS

PROJECT DATA:

ADDRESS
1426 S MAIN ST
WALNUT CREEK, CA 94596

APN
183-030-005

LOT SIZE
22,134 SF

BUILDING SIZE

EXISTING BUILDING:	3727 SF
PROPOSED ADDITION:	3216 SF
TOTAL:	6943 SF

LOT COVERAGE

EXISTING:	3727 / 22134 = 17%
PROPOSED:	6943 / 22134 = 31%

SETBACK CALCULATIONS:

REQUIRED:
25' AVG. SETBACK
25'x96' = 2400 SF REQUIRED

PROVIDED:
5' x 56' = 280 SF
20' x 47' = 940 SF
TOTAL: 1180 SF

PARKING REQUIRED
1 SPACE/250 SF OF RETAIL:

EXISTING: 3727 SF


PROPOSED: 3216 SF (ADDITION) + 3727 SF = 6943 SF

PARKING REQUIRED: 28 STALLS

3 STUDIO APARTMENTS x 1.25 STALLS = 3.75
2 ONE-BEDROOM x 1.5 STALLS = 3

TOTAL STALLS REQUIRED: 35

TOTAL STALLS PROVIDED: 23

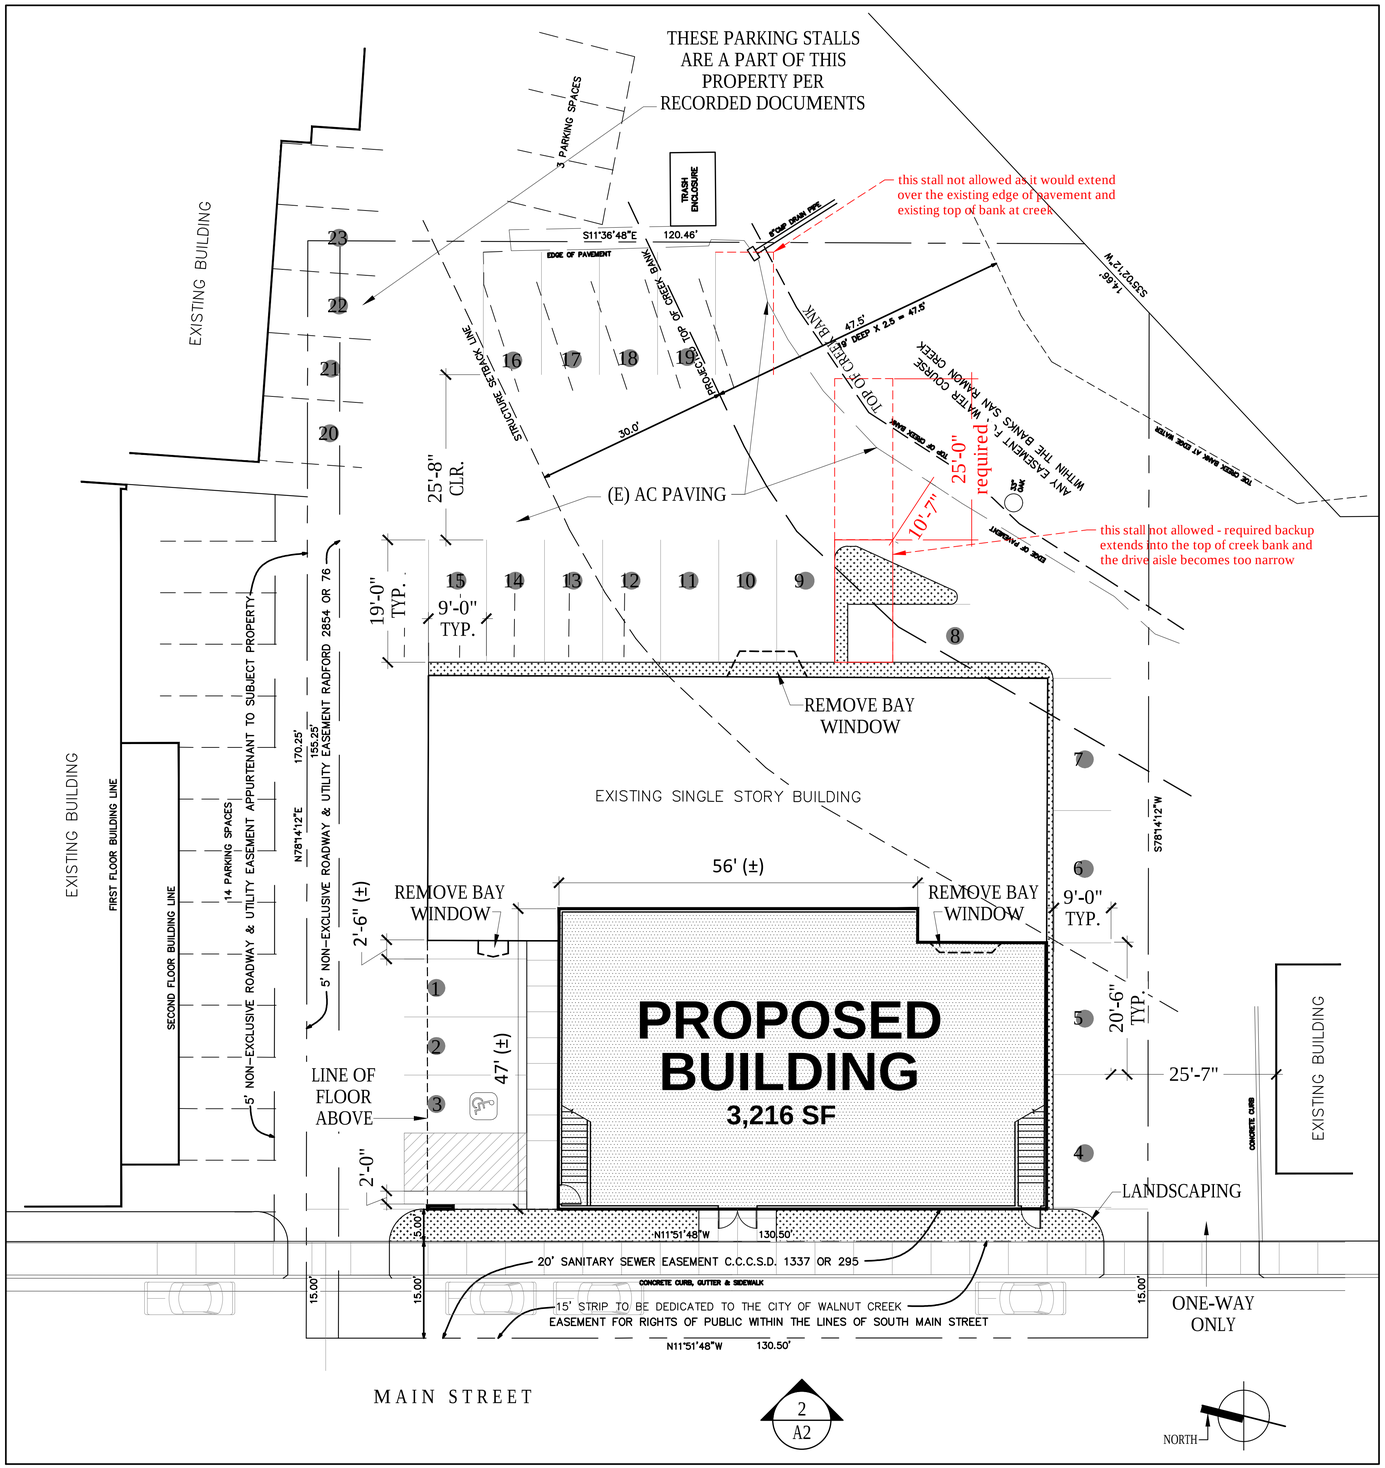

1 SITE PLAN

SCALE: 3/32" = 1'-0"

10'-8" 0' 10'-8" 21'-4"
SCALE: 3/32" = 1'-0"

LCA ARCHITECTS

WWW . LCA - ARCHITECTS . COM

CARL E. CAMPOS
DAVID BOGSTAD
PETER STACKPOLE

590 YGNACIO VALLEY ROAD, SUITE 310
WALNUT CREEK, CALIFORNIA 94596
(925) 944-1626

1970 BROADWAY, SUITE 800
OAKLAND, CALIFORNIA 94612
(510) 272-1060

1426 S. MAIN ST
RETAIL & RESIDENTIAL ADDITION

LCA ARCHITECTS
RESTRICTED ARCHITECTURAL DRAWINGS

THE INFORMATION, PLANS, DESIGNS, NOTES AND ARRANGEMENTS SHOWN ON THIS DRAWING ARE CONFIDENTIAL AND MAY NOT BE REPRODUCED IN WHOLE OR IN PART WITHOUT THE EXPRESSED WRITTEN PERMISSION OF LCA ARCHITECTS. DRAWINGS NOTED AS PRELIMINARY, SCHEMATIC AND / OR CONCEPT CONTAIN INFORMATION THAT IS CONCEPTUAL AND SUBJECT TO VERIFICATION AND/OR CHANGE. THE ARCHITECT MAKES NO CLAIM FOR ACCURACY OF CONCEPTUAL INFORMATION OR OF INFORMATION SUPPLIED BY OTHERS.

SITE PLAN

SCALE: AS NOTED
DATE: 10 / 08 / 19

REVISIONS:

PROJECT NO. 13034

A1

SHEET OF