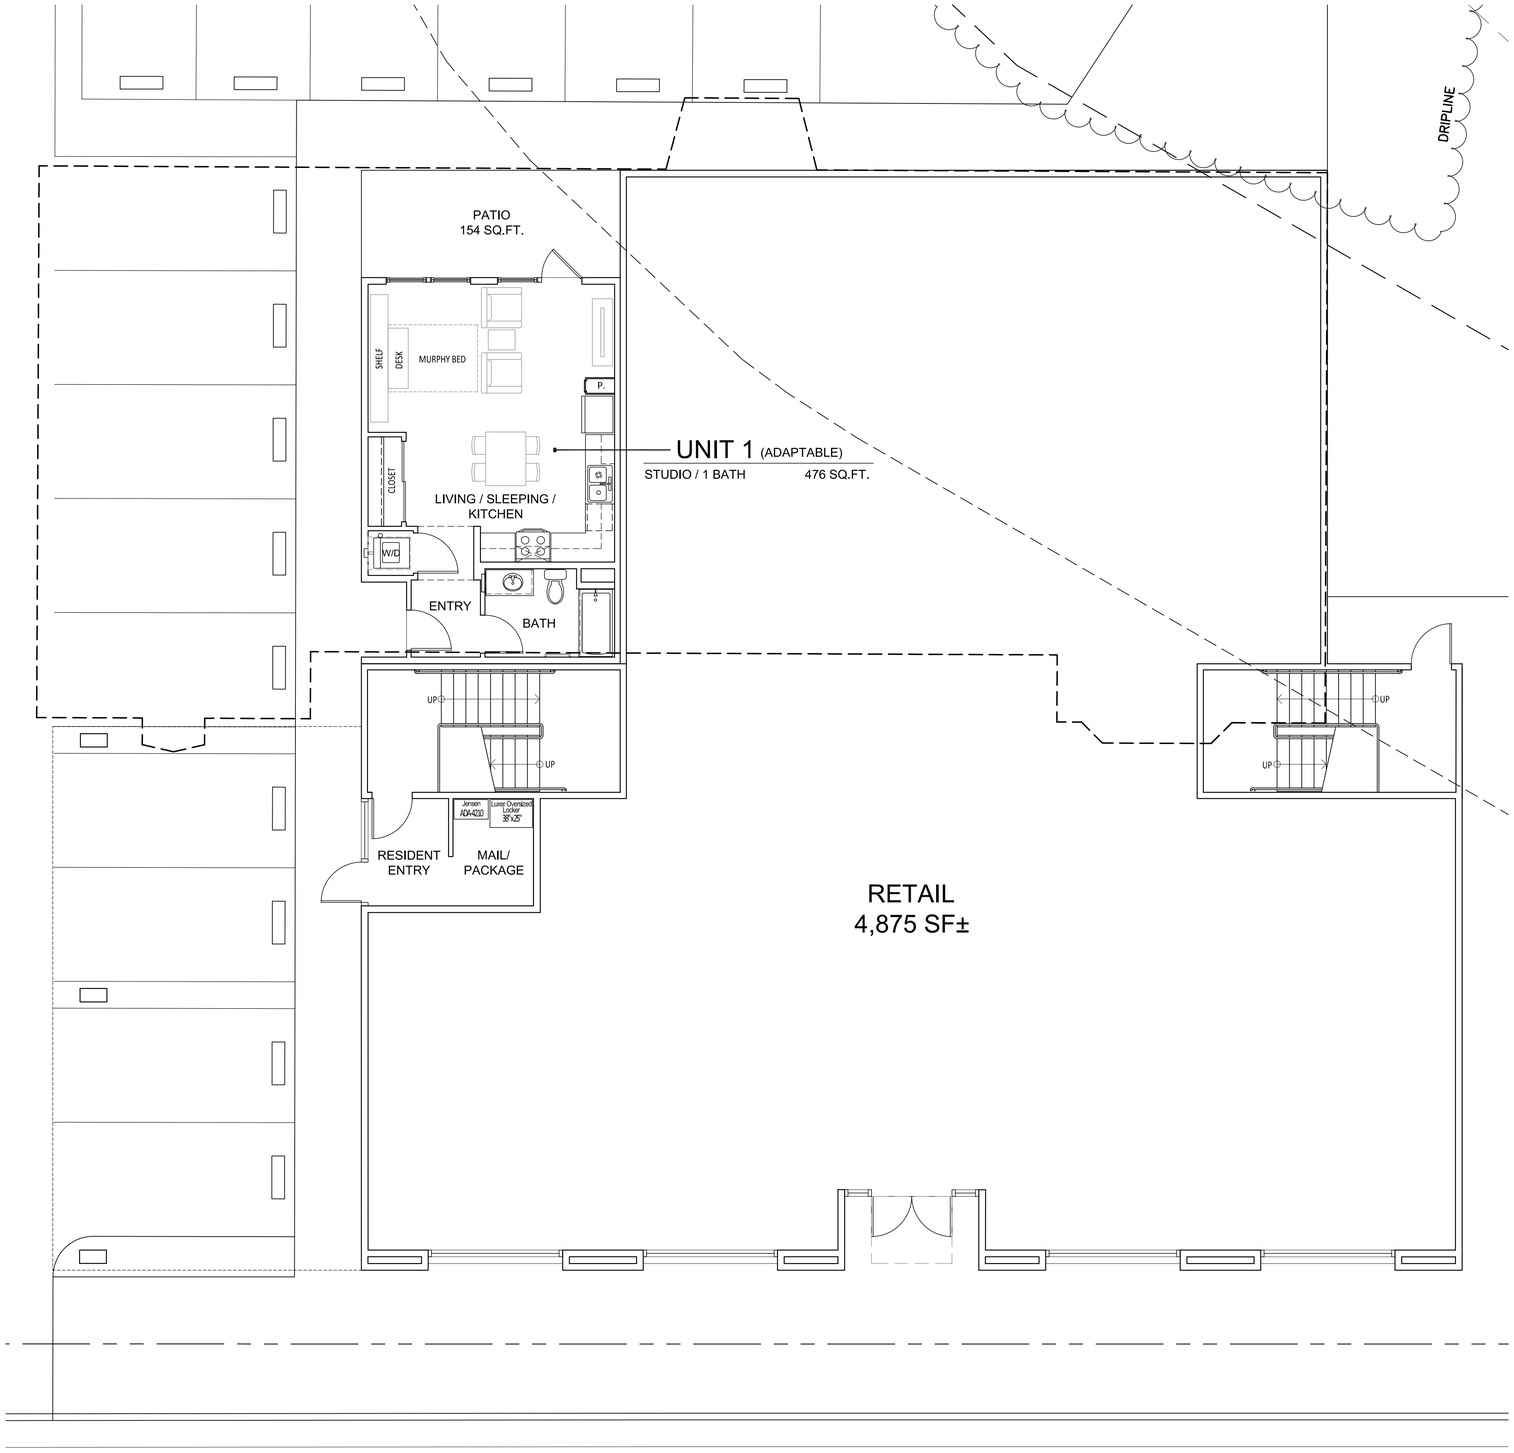


CONCEPTUAL GROUND LEVEL PLAN

4' 0' 4' 12'

SCALE: 3/16" = 1'-0"

LCA ARCHITECTS

WWW . LCA - ARCHITECTS . COM

CARL E. CAMPOS
DAVID BOGSTAD
PETER STACKPOLE

590 YGNACIO VALLEY ROAD, SUITE 310
WALNUT CREEK, CALIFORNIA 94596
(925) 944-1626

1970 BROADWAY, SUITE 800
OAKLAND, CALIFORNIA 94612
(510) 272-1060

1426 S. MAIN ST

RETAIL & RESIDENTIAL ADDITION

LCA ARCHITECTS
RESTRICTED ARCHITECTURAL DRAWINGS

THE INFORMATION, PLANS, DESIGNS, NOTES AND ARRANGEMENTS SHOWN ON THIS DRAWING ARE CONFIDENTIAL AND MAY NOT BE REPRODUCED IN WHOLE OR IN PART WITHOUT THE EXPRESSED WRITTEN PERMISSION OF LCA ARCHITECTS. DRAWINGS NOTED AS PRELIMINARY, SCHEMATIC AND / OR CONCEPT CONTAIN INFORMATION THAT IS CONCEPTUAL AND SUBJECT TO VERIFICATION AND/OR CHANGE. THE ARCHITECT MAKES NO CLAIM FOR ACCURACY OF CONCEPTUAL INFORMATION OR OF INFORMATION SUPPLIED BY OTHERS.

CONCEPTUAL GROUND LEVEL PLAN


SCALE:

DATE: 08 / 02 / 2021

REVISIONS:

PROJECT NO. 13034

SHEET OF

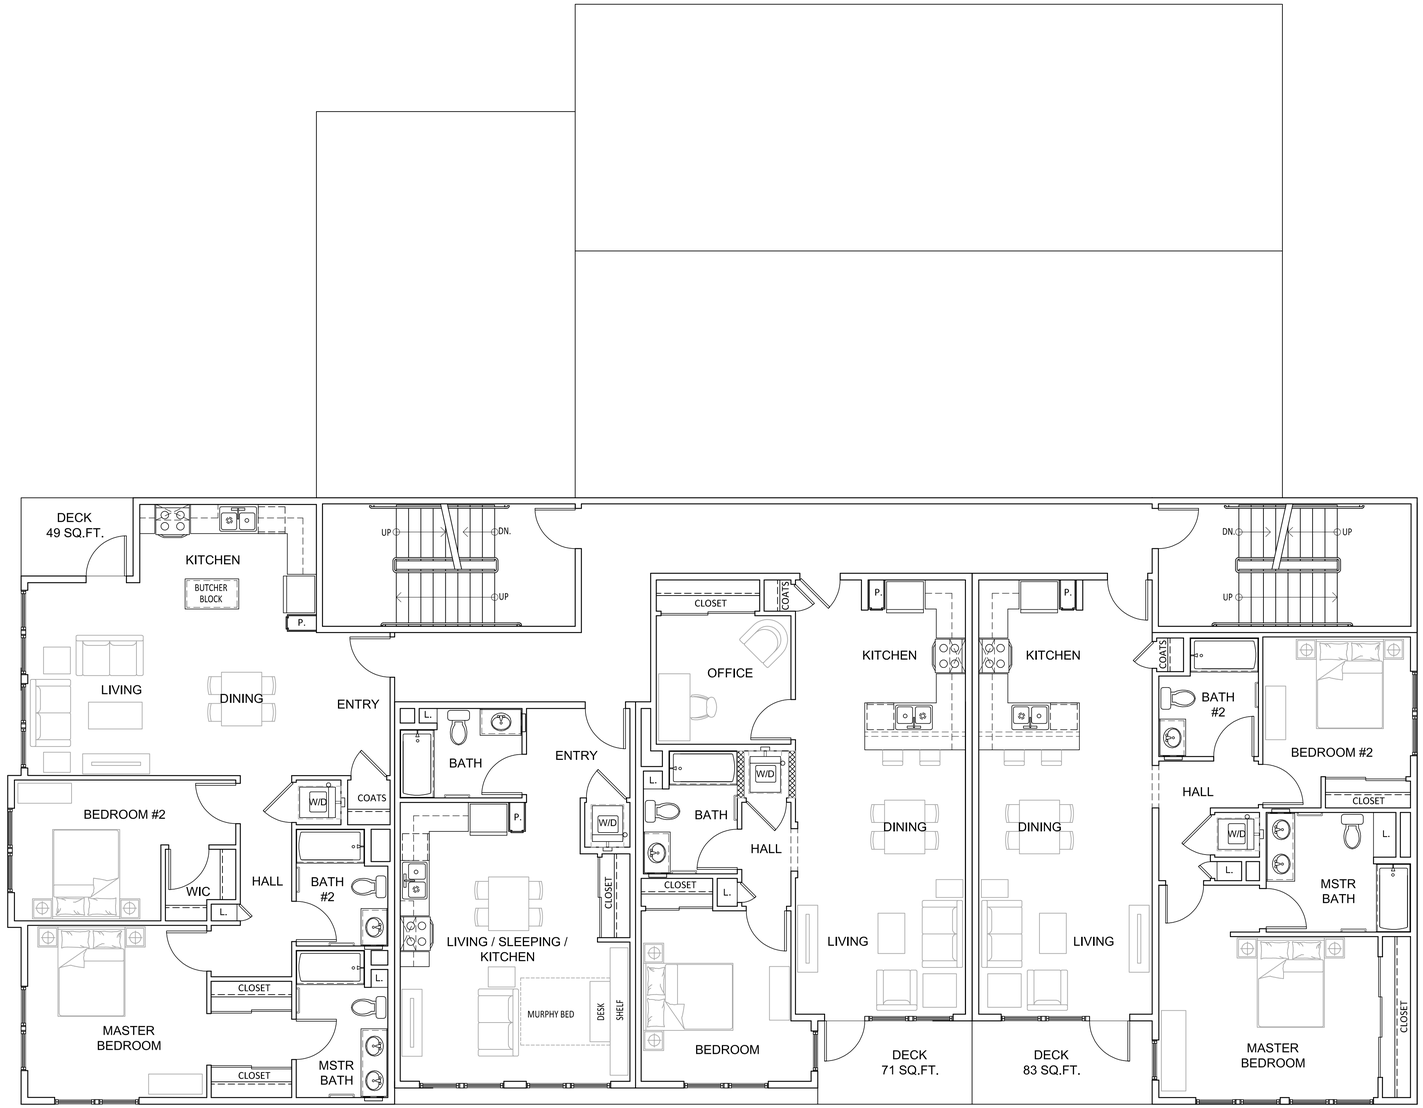

UNIT 2
2 BEDROOM / 2 BATH 1,100 SQ.FT.

UNIT 3
STUDIO / 1 BATH 476 SQ.FT.

UNIT 4
1 BEDROOM / OFFICE / 1 BATH 826 SQ.FT.

UNIT 5
2 BEDROOM / 2 BATH 1,076 SQ.FT.

CONCEPTUAL SECOND LEVEL PLAN

4' 0' 4' 12'
SCALE: 3/16" = 1'-0"

LCA ARCHITECTS

WWW . LCA - ARCHITECTS . COM

CARL E. CAMPOS
DAVID BOGSTAD
PETER STACKPOLE

590 YGNACIO VALLEY ROAD, SUITE 310
WALNUT CREEK, CALIFORNIA 94596
(925) 944-1626

1970 BROADWAY, SUITE 800
OAKLAND, CALIFORNIA 94612
(510) 272-1060

1426 S. MAIN ST
RETAIL & RESIDENTIAL ADDITION

LCA ARCHITECTS
RESTRICTED ARCHITECTURAL DRAWINGS


THE INFORMATION, PLANS, DESIGNS, NOTES AND ARRANGEMENTS SHOWN ON THIS DRAWING ARE CONFIDENTIAL AND MAY NOT BE REPRODUCED IN WHOLE OR IN PART WITHOUT THE EXPRESSED WRITTEN PERMISSION OF LCA ARCHITECTS. DRAWINGS NOTED AS PRELIMINARY, SCHEMATIC AND / OR CONCEPT CONTAIN INFORMATION THAT IS CONCEPTUAL AND SUBJECT TO VERIFICATION AND/OR CHANGE. THE ARCHITECT MAKES NO CLAIM FOR ACCURACY OF CONCEPTUAL INFORMATION OR OF INFORMATION SUPPLIED BY OTHERS.

CONCEPTUAL SECOND LEVEL PLAN

SCALE:
DATE: 08 / 02 / 2021
REVISIONS:

PROJECT NO. 13034

SHEET OF

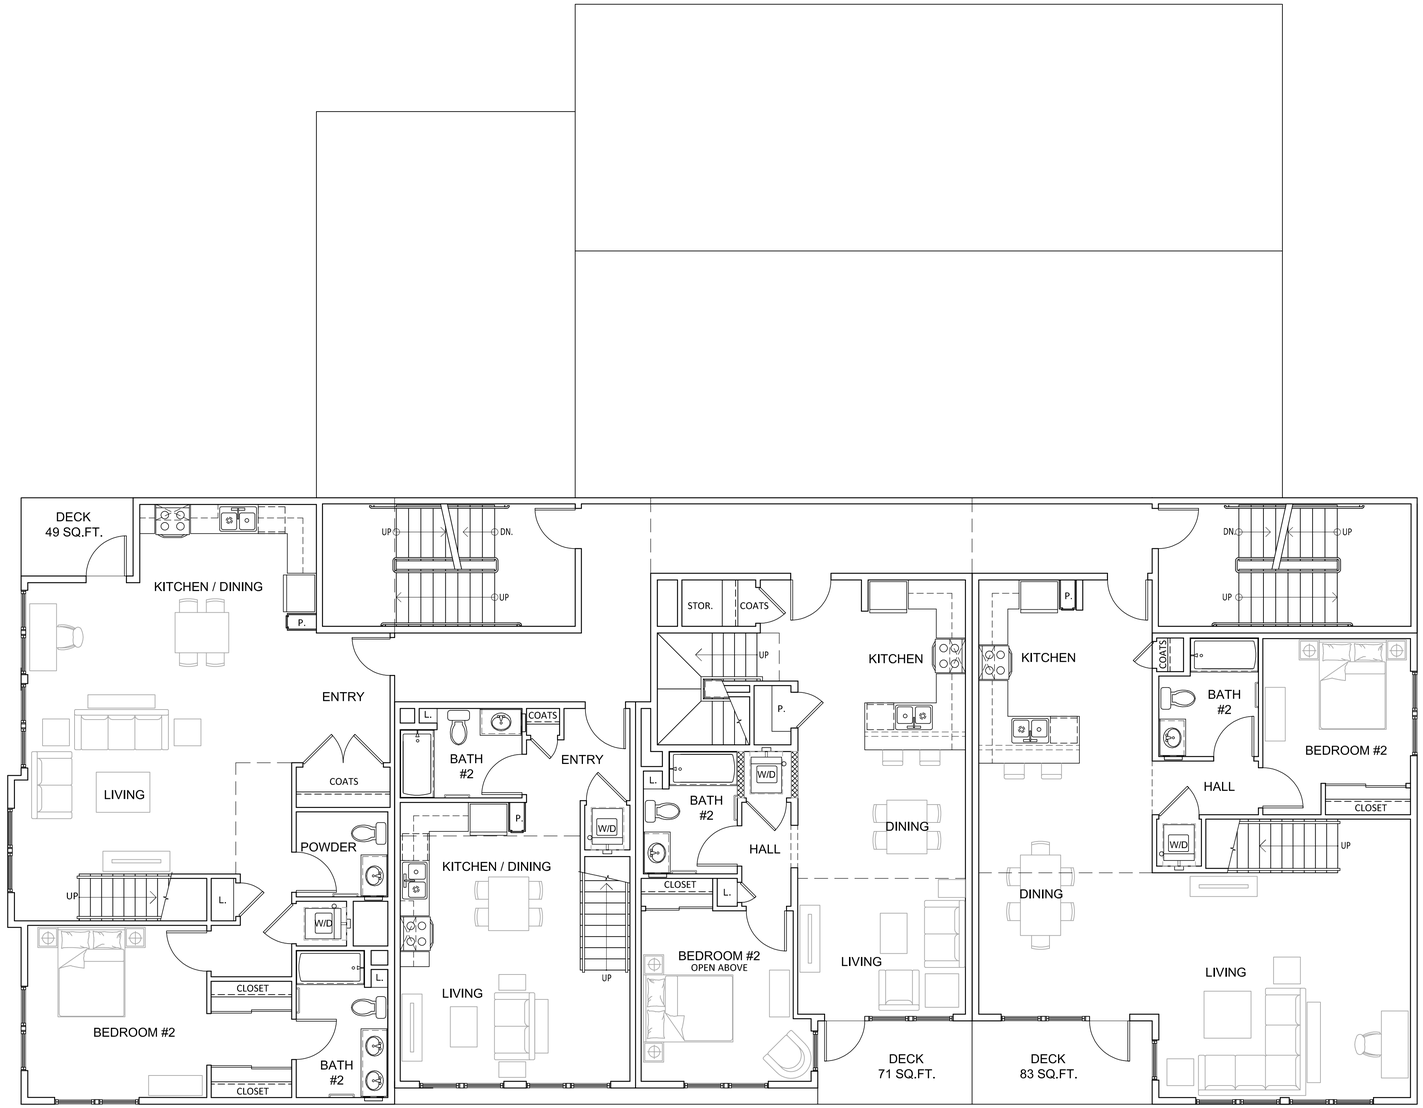

UNIT 6 - FIRST FLR
2 BEDROOM / 2.5 BATH 1,100 SQ.FT.
TOTAL = 1,587 SQ.FT.

UNIT 7 - FIRST FLR
1 BEDROOM / 2 BATH 476 SQ.FT.
TOTAL = 712 SQ.FT.

UNIT 8 - FIRST FLR
2 BEDROOM / 2 BATH 826 SQ.FT.
TOTAL = 1,239 SQ.FT.

UNIT 9 - FIRST FLR
2 BEDROOM / 2 BATH 1,076 SQ.FT.
TOTAL = 1,587 SQ.FT.

CONCEPTUAL THIRD LEVEL PLAN

4' 0' 4' 12'
SCALE: 3/16" = 1'-0"

LCA ARCHITECTS

WWW . LCA - ARCHITECTS . COM

CARL E. CAMPOS
DAVID BOGSTAD
PETER STACKPOLE

590 YGNACIO VALLEY ROAD, SUITE 310
WALNUT CREEK, CALIFORNIA 94596
(925) 944-1626

1970 BROADWAY, SUITE 800
OAKLAND, CALIFORNIA 94612
(510) 272-1060

1426 S. MAIN ST
RETAIL & RESIDENTIAL ADDITION

LCA ARCHITECTS
RESTRICTED ARCHITECTURAL DRAWINGS


THE INFORMATION, PLANS, DESIGNS, NOTES AND ARRANGEMENTS SHOWN ON THIS DRAWING ARE CONFIDENTIAL AND MAY NOT BE REPRODUCED IN WHOLE OR IN PART WITHOUT THE EXPRESSED WRITTEN PERMISSION OF LCA ARCHITECTS. DRAWINGS NOTED AS PRELIMINARY, SCHEMATIC AND / OR CONCEPT CONTAIN INFORMATION THAT IS CONCEPTUAL AND SUBJECT TO VERIFICATION AND/OR CHANGE. THE ARCHITECT MAKES NO CLAIM FOR ACCURACY OF CONCEPTUAL INFORMATION OR OF INFORMATION SUPPLIED BY OTHERS.

CONCEPTUAL
THIRD LEVEL
PLAN

SCALE:
DATE: 08 / 02 / 2021
REVISIONS:

PROJECT NO. 13034

SHEET OF

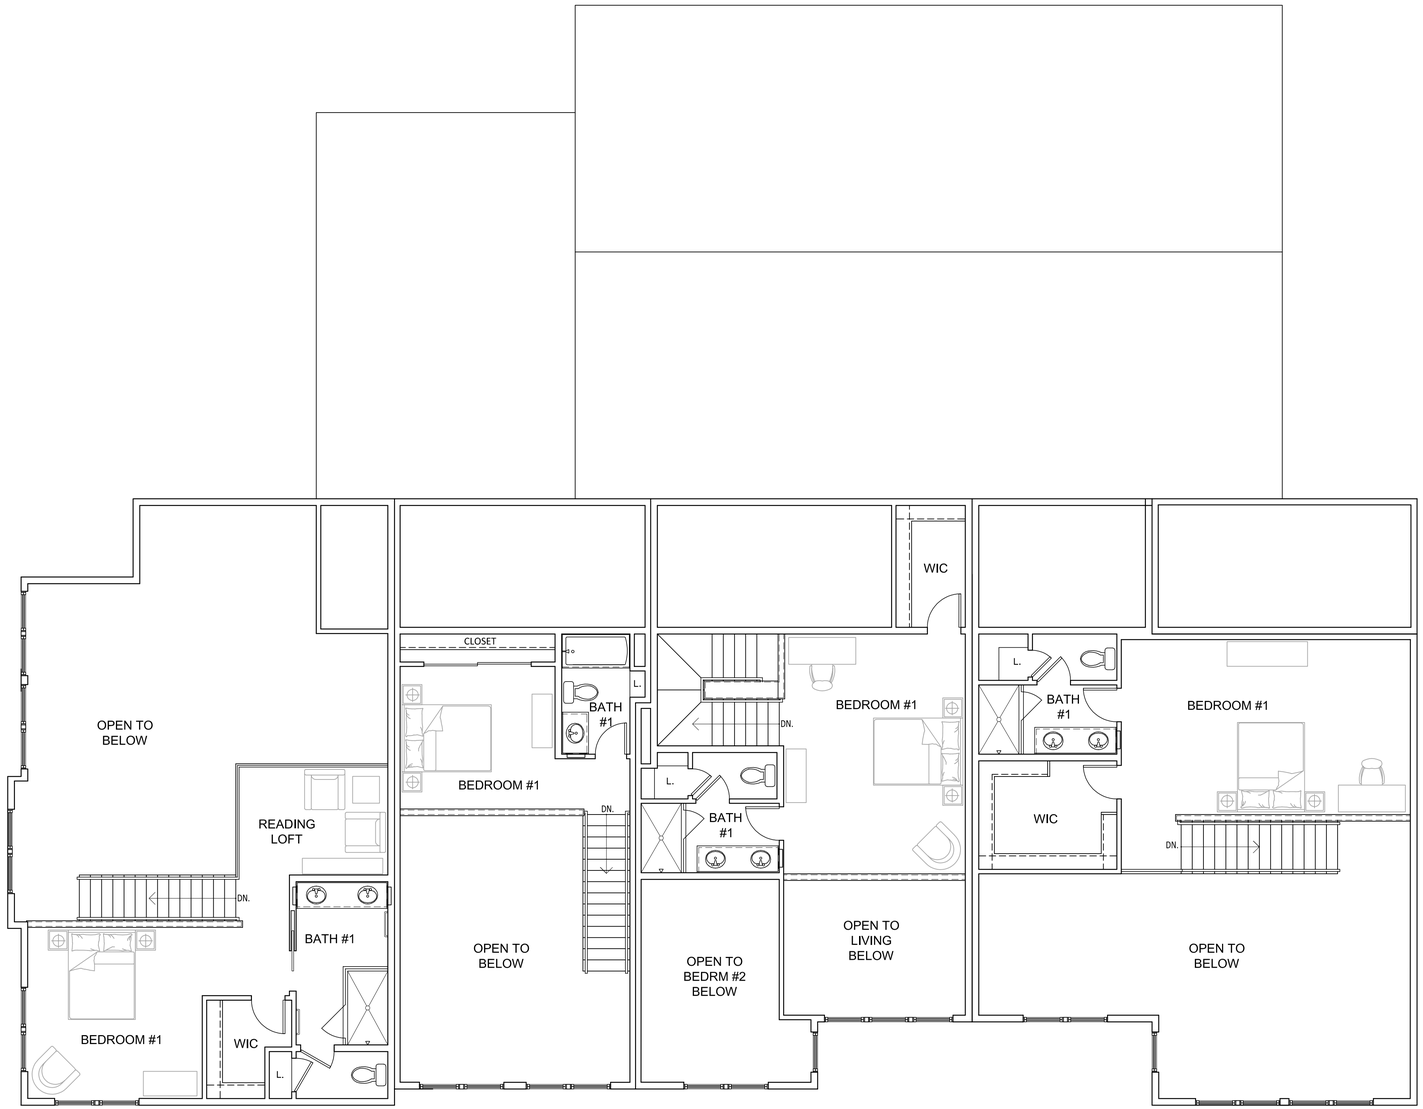

UNIT 6 - LOFT FLR
487 SQ.FT.

UNIT 7 - LOFT FLR
236 SQ.FT.

UNIT 8 - LOFT FLR
413 SQ.FT.

UNIT 9 - LOFT FLR
511 SQ.FT.

CONCEPTUAL LOFT LEVEL PLAN

4' 0' 4' 12'
SCALE: 3/16" = 1'-0"

LCA ARCHITECTS

WWW . LCA - ARCHITECTS . COM

CARL E. CAMPOS
DAVID BOGSTAD
PETER STACKPOLE

590 YGNACIO VALLEY ROAD, SUITE 310
WALNUT CREEK, CALIFORNIA 94596
(925) 944-1626

1970 BROADWAY, SUITE 800
OAKLAND, CALIFORNIA 94612
(510) 272-1060

1426 S. MAIN ST

RETAIL & RESIDENTIAL ADDITION

LCA ARCHITECTS
RESTRICTED ARCHITECTURAL DRAWINGS

THE INFORMATION, PLANS, DESIGNS, NOTES AND ARRANGEMENTS SHOWN ON THIS DRAWING ARE CONFIDENTIAL AND MAY NOT BE REPRODUCED IN WHOLE OR IN PART WITHOUT THE EXPRESSED WRITTEN PERMISSION OF LCA ARCHITECTS. DRAWINGS NOTED AS PRELIMINARY, SCHEMATIC AND / OR CONCEPT CONTAIN INFORMATION THAT IS CONCEPTUAL AND SUBJECT TO VERIFICATION AND/OR CHANGE. THE ARCHITECT MAKES NO CLAIM FOR ACCURACY OF CONCEPTUAL INFORMATION OR OF INFORMATION SUPPLIED BY OTHERS.

CONCEPTUAL
LOFT LEVEL
PLAN

SCALE:
DATE: 08 / 02 / 2021
REVISIONS:

PROJECT NO. 13034

SHEET OF