1426 S. MAIN ST

PROPOSED ADDITION OF RETAIL SPACE AND 9 NEW RESIDENTIAL UNITS W/ NEW LANDSCAPING

PROJECT DATA:

ADDRESS
1426 S MAIN ST
WALNUT CREEK, CA 94596

APN
183-030-005

ZONING
CR: CENTRAL RETAIL

GENERAL PLAN
GR: GENERAL RETAIL

SPECIFIC PLAN
SP-7 SOUTH NEWELL AVENUE

LOT SIZE
22,134 SF

BUILDING GROSS FLOOR AREA

EXISTING BUILDING:	3,727 SF±

PROPOSED BUILDING

GROUND LEVEL:	6,090 SF±
SECOND LEVEL:	4,474 SF±
THIRD LEVEL:	4,474 SF±
FOURTH LEVEL:	1,830 SF±
PROPOSED TOTAL:	16,868 SF±

LOT COVERAGE

EXISTING:	$\frac{3727}{22134}$ = 17%
PROPOSED:	$\frac{7161}{22134}$ = 32%
ALLOWED:	NO RESTRICTIONS

UNIT MIX

STUDIO UNITS:	2 UNITS
ONE BEDROOM UNITS:	2 UNITS
TWO BEDROOM UNITS:	5 UNITS
TOTAL UNITS:	9 UNITS

DENSITY BONUS
PROPOSED VERY LOW
INCOME AFFORDABLE UNITS: 1 UNIT (11% OF TOTAL)

INCENTIVES / CONCESSIONS: 2

PARKING REQUIRED

PROPOSED RETAIL NET RENTABLE AREA =	4,875 SF±
RETAIL PARKING REQUIRED (1 PER 250 SF):	20 STALLS


RESIDENTIAL PARKING (DENSITY BONUS STANDARD)

2 STUDIO APARTMENT (1 PER UNIT):	2 STALLS
1 ONE BEDROOM APARTMENT (1 PER UNIT):	2 STALL
2 TWO BEDROOM APARTMENTS (1.5 PER UNIT):	7.5 STALLS
TOTAL RESIDENTIAL PARKING REQUIRED:	12 STALLS
TOTAL PARKING REQUIRED:	32 PARKING STALLS
TOTAL PARKING PROVIDED:	24 PARKING STALLS

(PROPOSED PARKING REQUIREMENT REDUCTION THROUGH DENSITY BONUS INCENTIVE AND/OR PARKING STUDY OF REQUIREMENTS FOR ADIB'S PERSIAN RUG)

EXISTING STREET VIEW FROM SOUTH MAIN:



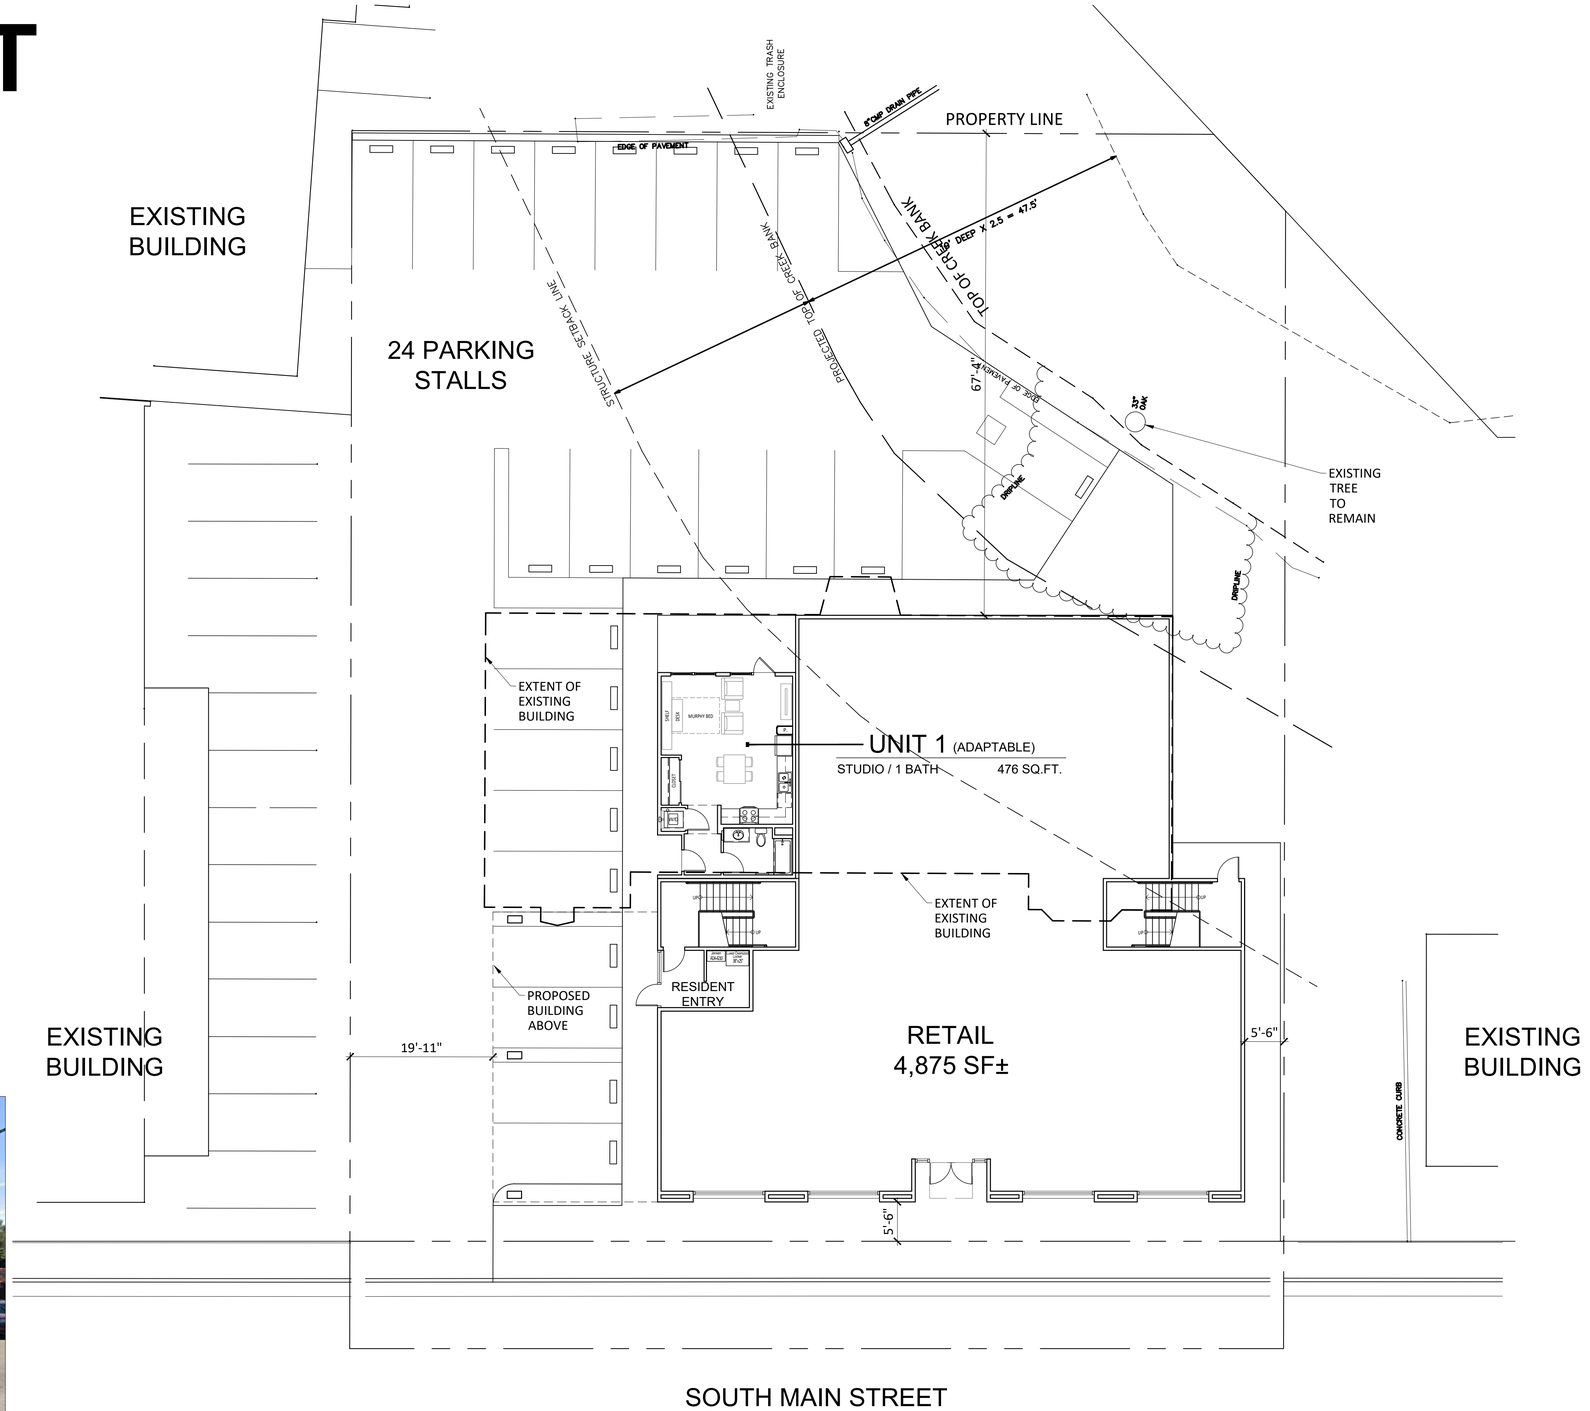

CONCEPTUAL SITE PLAN

10' 0' 10' 20'
SCALE: 1" = 10'-0"
NORTH

LCA ARCHITECTS

WWW . LCA - ARCHITECTS . COM

CARL E. CAMPOS
DAVID BOGSTAD
PETER STACKPOLE

590 YGNACIO VALLEY ROAD, SUITE 310
WALNUT CREEK, CALIFORNIA 94596
(925) 944-1626

1970 BROADWAY, SUITE 800
OAKLAND, CALIFORNIA 94612
(510) 272-1060

1426 S. MAIN ST
RETAIL & RESIDENTIAL ADDITION

LCA ARCHITECTS
RESTRICTED ARCHITECTURAL DRAWINGS


THE INFORMATION, PLANS, DESIGNS, NOTES AND ARRANGEMENTS SHOWN ON THIS DRAWING ARE CONFIDENTIAL, AND MAY NOT BE REPRODUCED IN WHOLE OR IN PART WITHOUT THE EXPRESSED WRITTEN PERMISSION OF LCA ARCHITECTS. DRAWINGS NOTED AS PRELIMINARY, SCHEMATIC AND / OR CONCEPT CONTAIN INFORMATION THAT IS CONCEPTUAL AND SUBJECT TO VERIFICATION AND/OR CHANGE. THE ARCHITECT MAKES NO CLAIM FOR ACCURACY OF CONCEPTUAL INFORMATION OR OF INFORMATION SUPPLIED BY OTHERS.

CONCEPTUAL GROUND LEVEL PLAN

SCALE:
DATE: 09 / 09 / 2021
REVISIONS:

PROJECT NO. 13034

SHEET OF

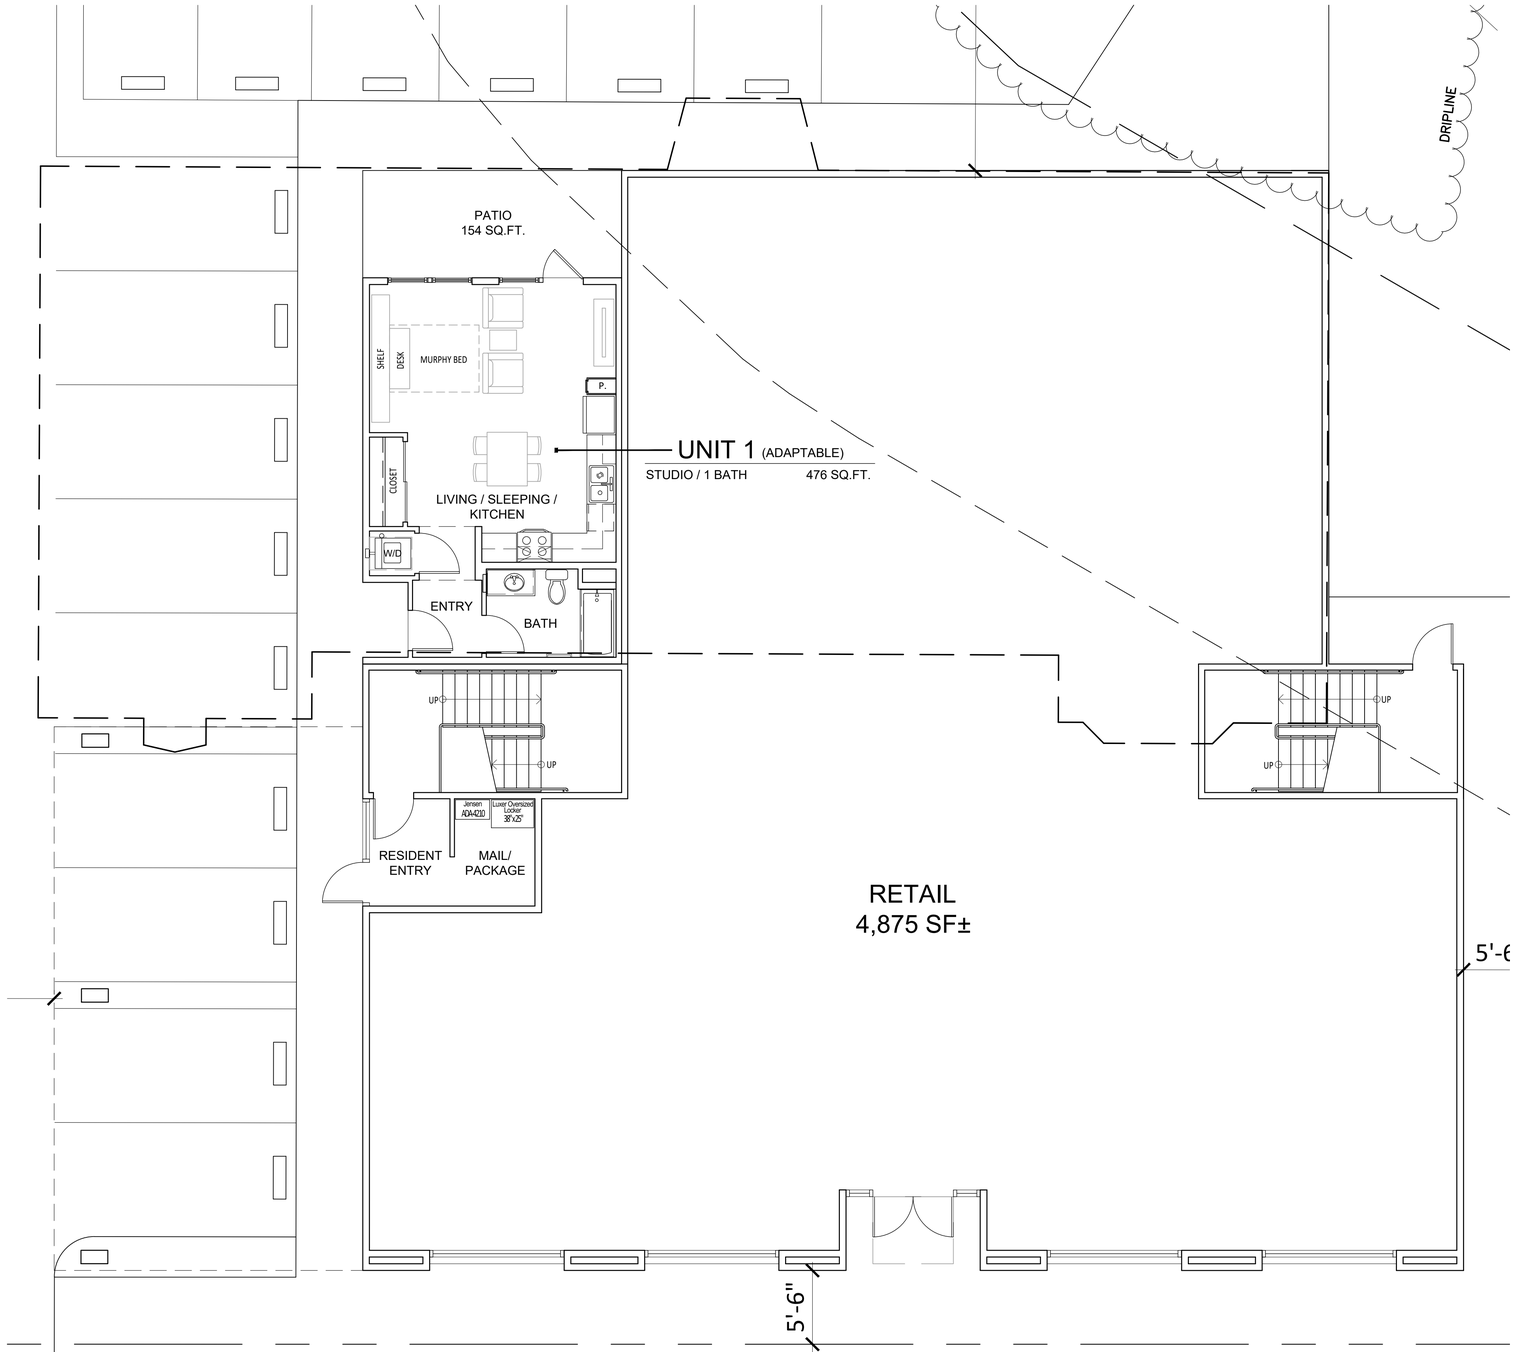

CONCEPTUAL GROUND LEVEL PLAN

4' 0' 4' 12'
SCALE: 3/16" = 1'-0"
NORTH

LCA ARCHITECTS

WWW . LCA - ARCHITECTS . COM

CARL E. CAMPOS
DAVID BOGSTAD
PETER STACKPOLE

590 YGNACIO VALLEY ROAD, SUITE 310
WALNUT CREEK, CALIFORNIA 94596
(925) 944-1626

1970 BROADWAY, SUITE 800
OAKLAND, CALIFORNIA 94612
(510) 272-1060

1426 S. MAIN ST

RETAIL & RESIDENTIAL ADDITION

LCA ARCHITECTS
RESTRICTED ARCHITECTURAL DRAWINGS


THE INFORMATION, PLANS, DESIGNS, NOTES AND ARRANGEMENTS SHOWN ON THIS DRAWING ARE CONFIDENTIAL AND MAY NOT BE REPRODUCED IN WHOLE OR IN PART WITHOUT THE EXPRESSED WRITTEN PERMISSION OF LCA ARCHITECTS. DRAWINGS NOTED AS PRELIMINARY, SCHEMATIC AND / OR CONCEPT CONTAIN INFORMATION THAT IS CONCEPTUAL AND SUBJECT TO VERIFICATION AND/OR CHANGE. THE ARCHITECT MAKES NO CLAIM FOR ACCURACY OF CONCEPTUAL INFORMATION OR OF INFORMATION SUPPLIED BY OTHERS.

CONCEPTUAL GROUND LEVEL PLAN

SCALE:
DATE: 09 / 09 / 2021
REVISIONS:

PROJECT NO. 13034

SHEET OF

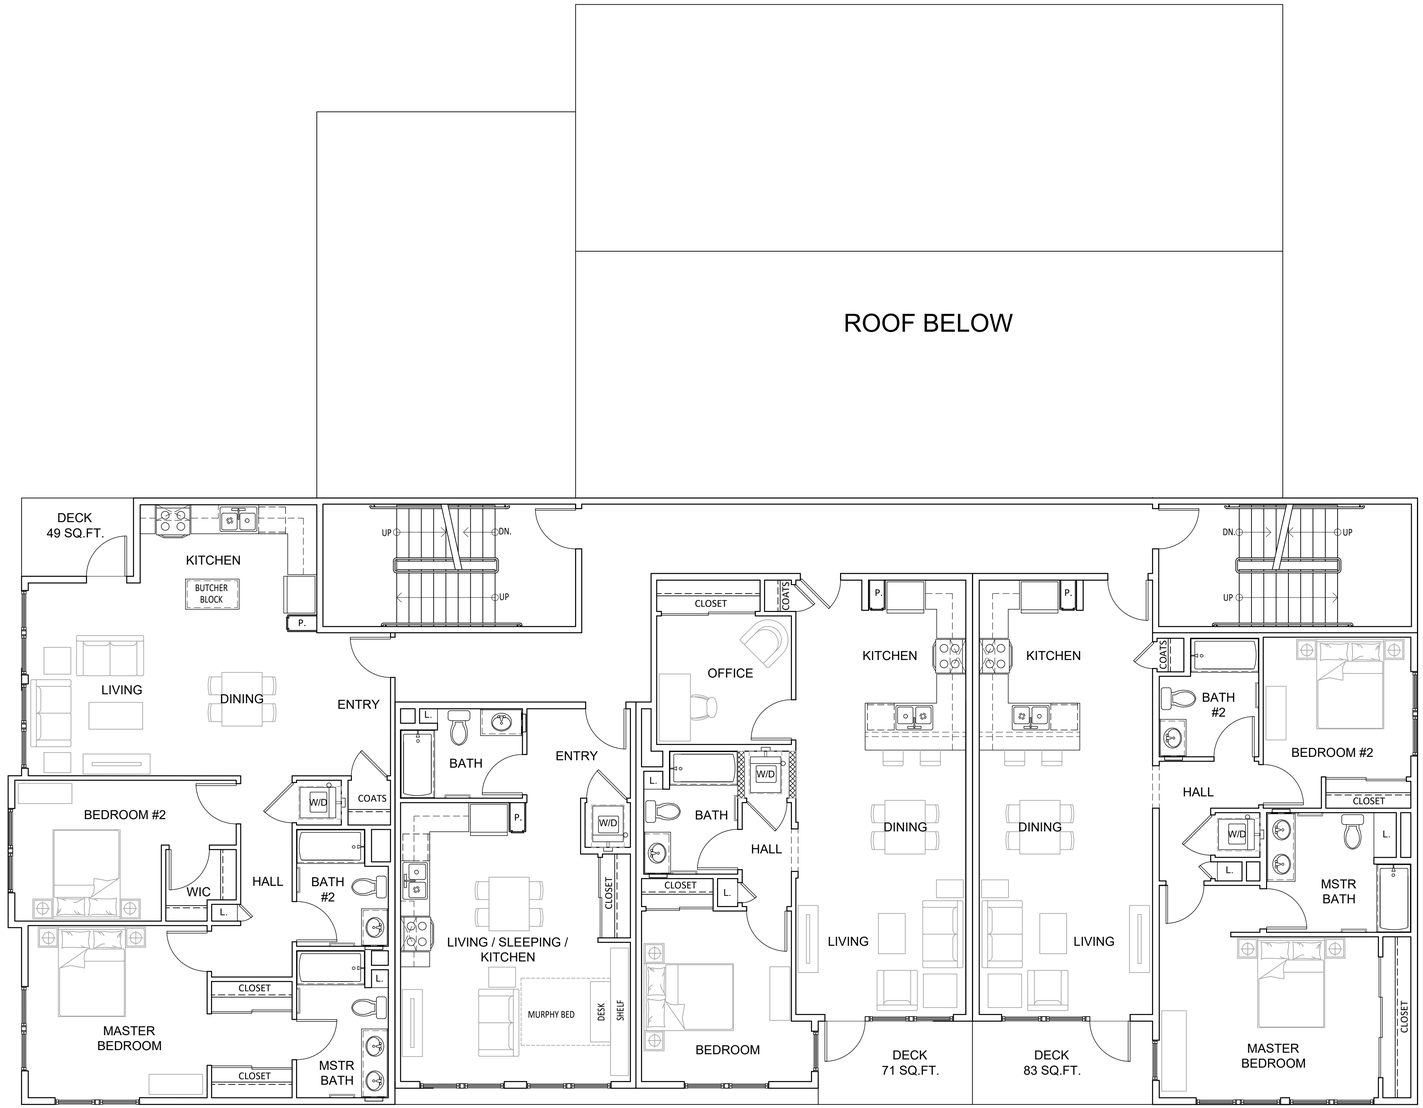

UNIT 2

2 BEDROOM / 2 BATH 1,100 SQ.FT.

UNIT 3

STUDIO / 1 BATH 476 SQ.FT.

UNIT 4

1 BEDROOM / OFFICE / 1 BATH 826 SQ.FT.

UNIT 5

2 BEDROOM / 2 BATH 1,076 SQ.FT.

CONCEPTUAL SECOND LEVEL PLAN

4' 0' 4' 12' NORTH

SCALE: 3/16" = 1'-0"

LCA ARCHITECTS

WWW . LCA - ARCHITECTS . COM

CARL E. CAMPOS
DAVID BOGSTAD
PETER STACKPOLE

590 YGNACIO VALLEY ROAD, SUITE 310
WALNUT CREEK, CALIFORNIA 94596
(925) 944-1626

1970 BROADWAY, SUITE 800
OAKLAND, CALIFORNIA 94612
(510) 272-1060

1426 S. MAIN ST

RETAIL & RESIDENTIAL ADDITION

LCA ARCHITECTS
RESTRICTED ARCHITECTURAL DRAWINGS

THE INFORMATION, PLANS, DESIGNS, NOTES AND ARRANGEMENTS SHOWN ON THIS DRAWING ARE CONFIDENTIAL AND MAY NOT BE REPRODUCED IN WHOLE OR IN PART WITHOUT THE EXPRESSED WRITTEN PERMISSION OF LCA ARCHITECTS. DRAWINGS NOTED AS PRELIMINARY, SCHEMATIC AND / OR CONCEPT CONTAIN INFORMATION THAT IS CONCEPTUAL AND SUBJECT TO VERIFICATION AND/OR CHANGE. THE ARCHITECT MAKES NO CLAIM FOR ACCURACY OF CONCEPTUAL INFORMATION OR OF INFORMATION SUPPLIED BY OTHERS.

CONCEPTUAL
SECOND LEVEL
PLAN


SCALE:

DATE: 09 / 09 / 2021

REVISIONS:

PROJECT NO. 13034

SHEET OF

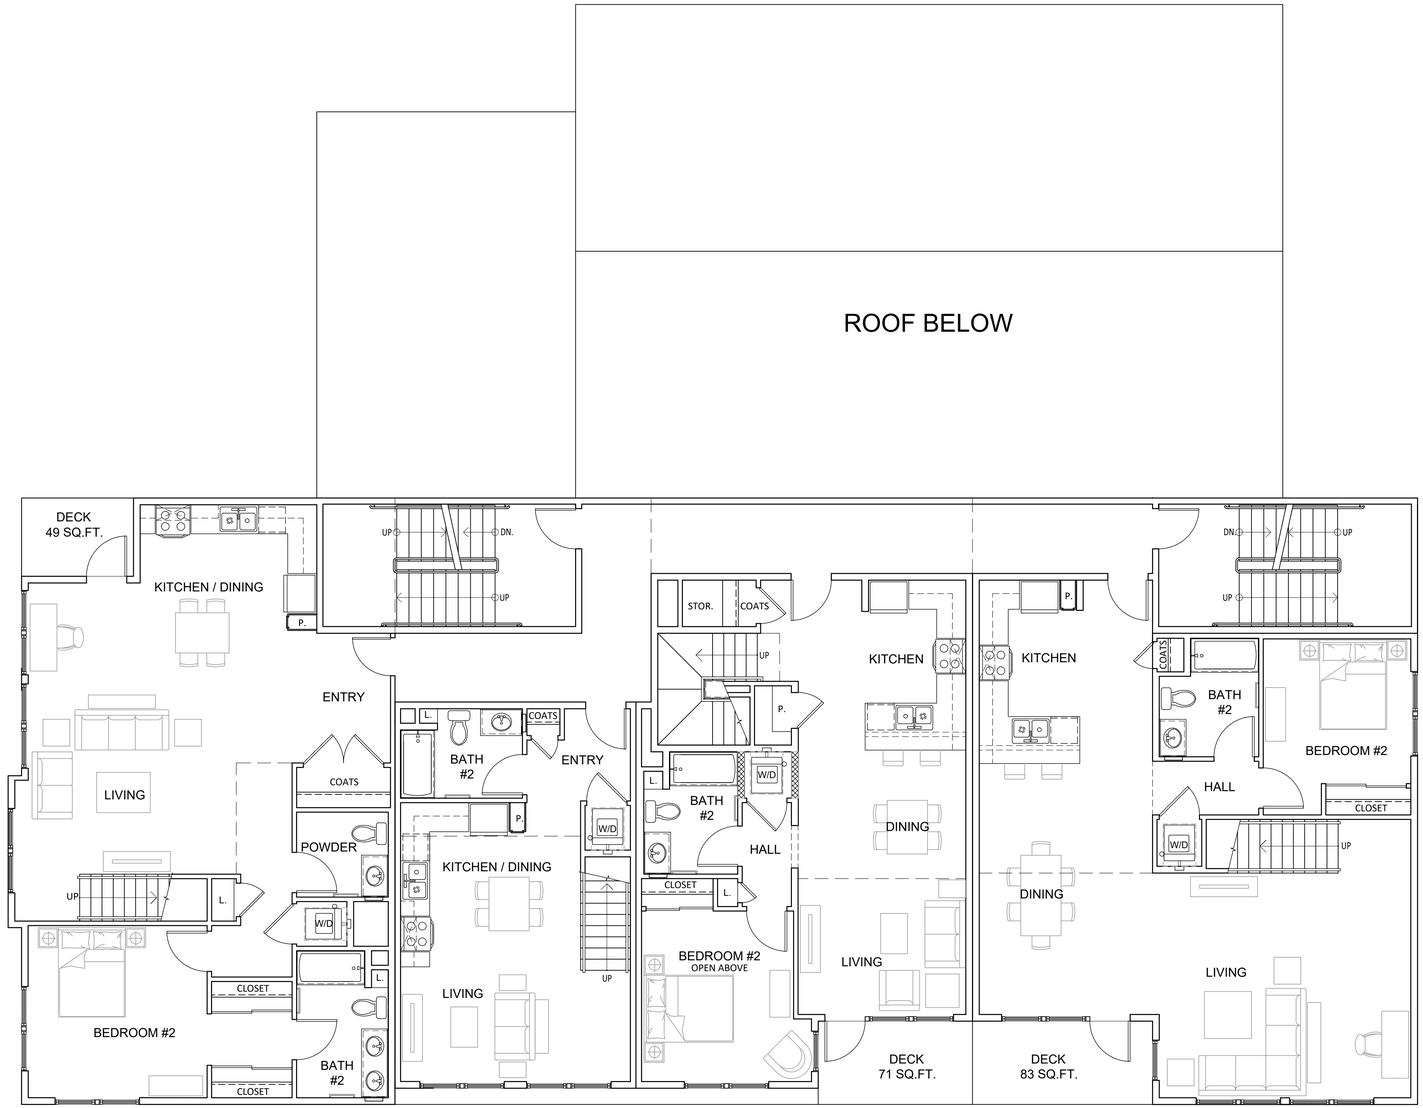

UNIT 6 - FIRST FLOOR

2 BEDROOM / 2.5 BATH

FIRST FLOOR	=	1,100 SF±
LOFT	=	487 SF±
TOTAL	=	1,587 SF±

UNIT 7 - FIRST FLOOR

1 BEDROOM / 2 BATH

FIRST FLOOR	=	476 SF±
LOFT	=	236 SF±
TOTAL	=	712 SF±.

UNIT 8 - FIRST FLOOR

2 BEDROOM / 2 BATH

FIRST FLOOR	=	826 SF±
LOFT	=	413 SF±
TOTAL	=	1,239 SF±.

UNIT 9 - FIRST FLOOR

2 BEDROOM / 2 BATH

FIRST FLOOR	=	1,076 SF±
LOFT	=	511 SF±
TOTAL	=	1,587 SF±

CONCEPTUAL THIRD LEVEL PLAN

4' 0' 4' 12'

SCALE: 3/16" = 1'-0"

NORTH

LCA ARCHITECTS

WWW . LCA - ARCHITECTS . COM

CARL E. CAMPOS
DAVID BOGSTAD
PETER STACKPOLE

590 YGNACIO VALLEY ROAD, SUITE 310
WALNUT CREEK, CALIFORNIA 94596
(925) 944-1626

1970 BROADWAY, SUITE 800
OAKLAND, CALIFORNIA 94612
(510) 272-1060

1426 S. MAIN ST

RETAIL & RESIDENTIAL ADDITION

LCA ARCHITECTS
RESTRICTED ARCHITECTURAL DRAWINGS

THE INFORMATION, PLANS, DESIGNS, NOTES AND ARRANGEMENTS SHOWN ON THIS DRAWING ARE CONFIDENTIAL AND MAY NOT BE REPRODUCED IN WHOLE OR IN PART WITHOUT THE EXPRESSED WRITTEN PERMISSION OF LCA ARCHITECTS. DRAWINGS NOTED AS PRELIMINARY, SCHEMATIC AND / OR CONCEPT CONTAIN INFORMATION THAT IS CONCEPTUAL AND SUBJECT TO VERIFICATION AND/OR CHANGE. THE ARCHITECT MAKES NO CLAIM FOR ACCURACY OF CONCEPTUAL INFORMATION OR OF INFORMATION SUPPLIED BY OTHERS.

CONCEPTUAL
THIRD LEVEL
PLAN


SCALE:

DATE: 09 / 09 / 2021

REVISIONS:

PROJECT NO. 13034

SHEET OF

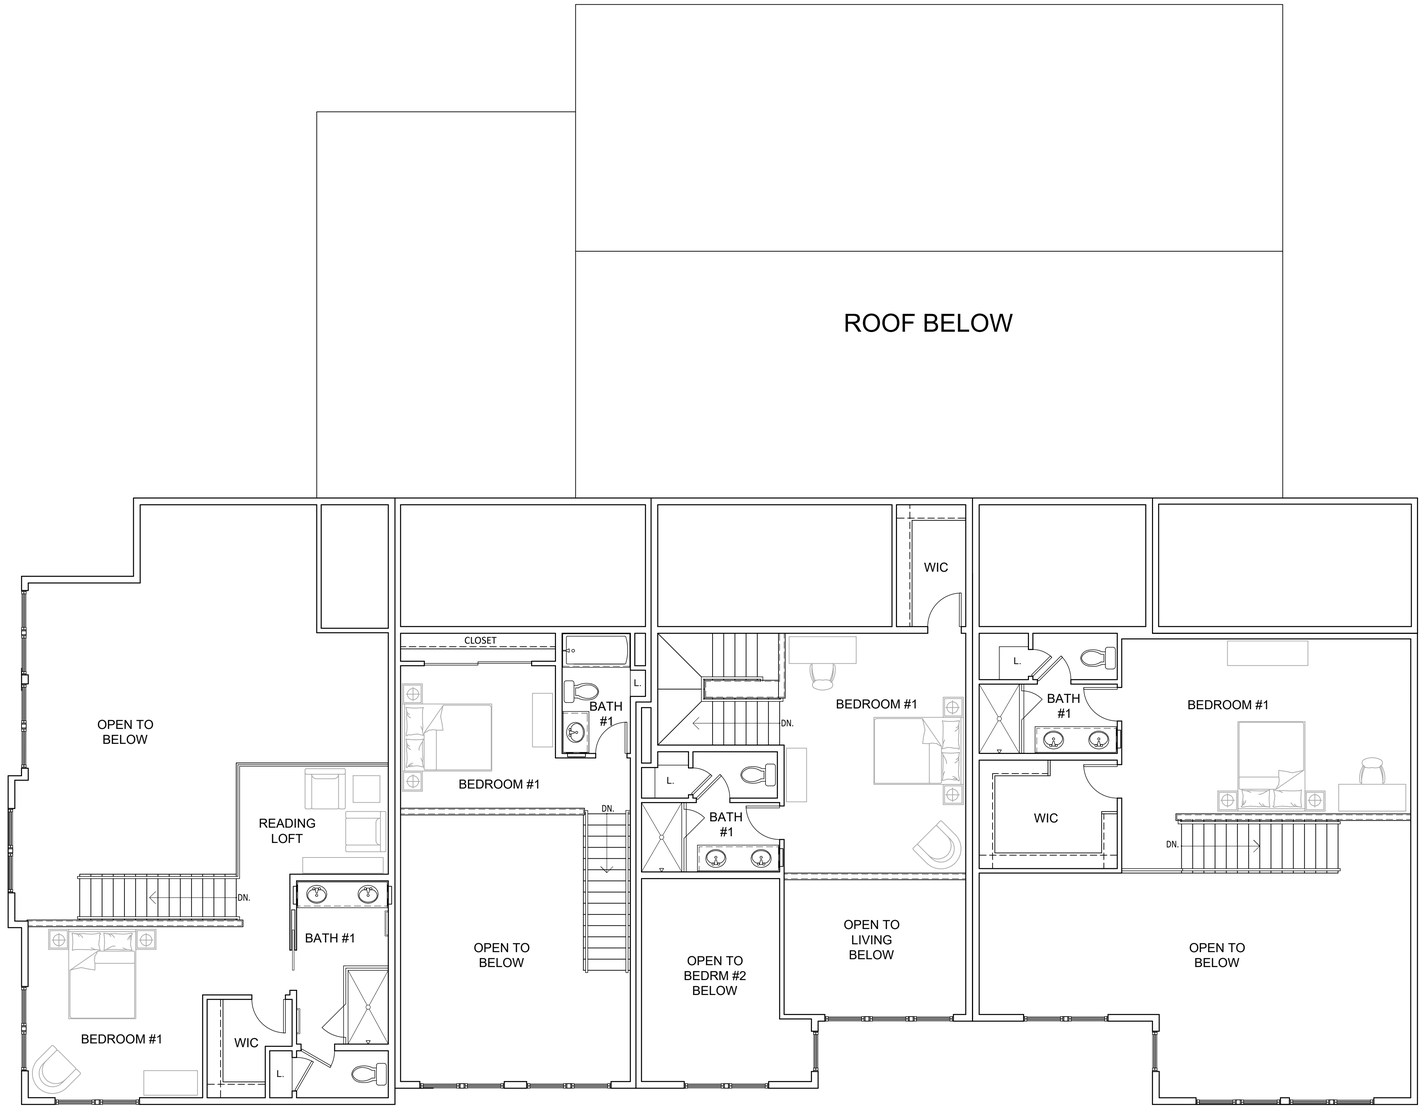

UNIT 6 - LOFT FLOOR
487 SF±

UNIT 7 - LOFT FLOOR
236 SF±

UNIT 8 - LOFT FLOOR
413 SF±

UNIT 9 - LOFT FLOOR
511 SF±

CONCEPTUAL LOFT LEVEL PLAN

4' 0' 4' 12'
SCALE: 3/16" = 1'-0"
NORTH

LCA ARCHITECTS

WWW . LCA - ARCHITECTS . COM

CARL E. CAMPOS
DAVID BOGSTAD
PETER STACKPOLE

590 YGNACIO VALLEY ROAD, SUITE 310
WALNUT CREEK, CALIFORNIA 94596
(925) 944-1626

1970 BROADWAY, SUITE 800
OAKLAND, CALIFORNIA 94612
(510) 272-1060

1426 S. MAIN ST
RETAIL & RESIDENTIAL ADDITION

LCA ARCHITECTS
RESTRICTED ARCHITECTURAL DRAWINGS

THE INFORMATION, PLANS, DESIGNS, NOTES AND ARRANGEMENTS SHOWN ON THIS DRAWING ARE CONFIDENTIAL, AND MAY NOT BE REPRODUCED IN WHOLE OR IN PART WITHOUT THE EXPRESSED WRITTEN PERMISSION OF LCA ARCHITECTS. DRAWINGS NOTED AS PRELIMINARY, SCHEMATIC AND / OR CONCEPT CONTAIN INFORMATION THAT IS CONCEPTUAL AND SUBJECT TO VERIFICATION AND/OR CHANGE. THE ARCHITECT MAKES NO CLAIM FOR ACCURACY OF CONCEPTUAL INFORMATION OR OF INFORMATION SUPPLIED BY OTHERS.

CONCEPTUAL
LOFT LEVEL
PLAN

SCALE:
DATE: 09 / 09 / 2021
REVISIONS:

PROJECT NO. 13034

SHEET OF